


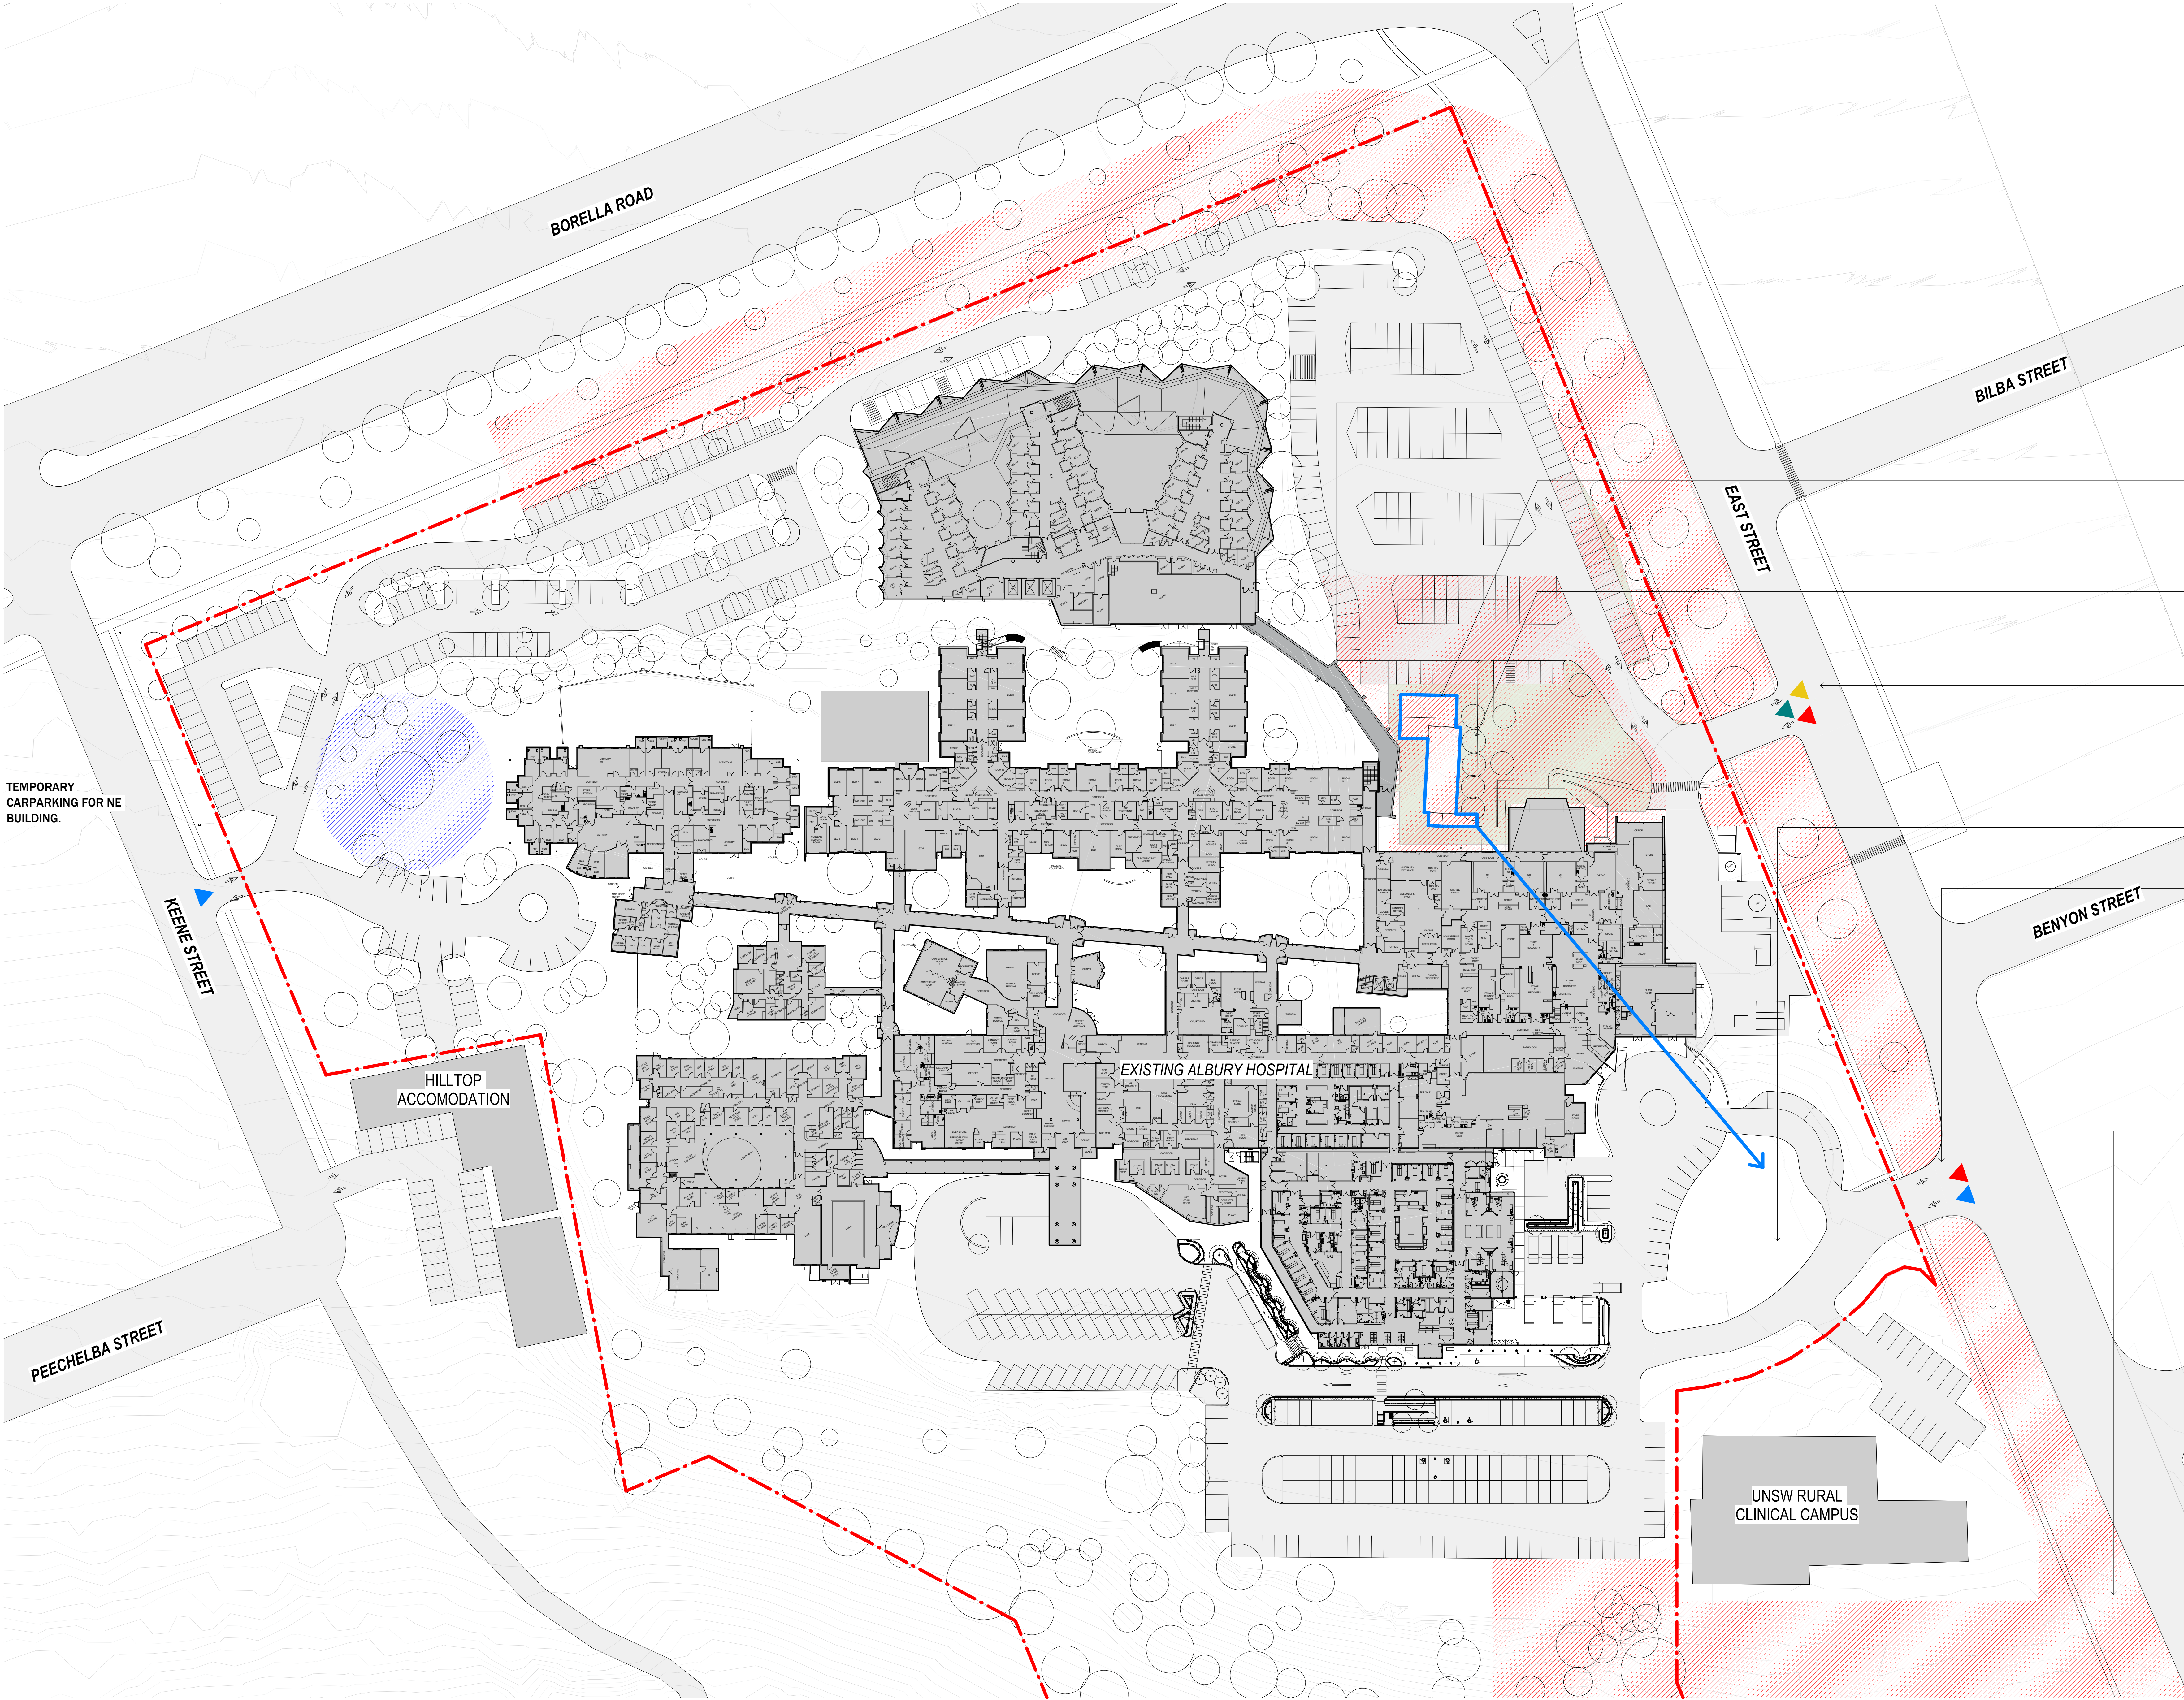

LEGEND:

- DEMOLITION / SITE PREPARATION
- TEMPORARY PARKING
- DECANT ON SITE
- DECANT OFF SITE
- NEW BUILD
- EXISTING
- PROTECTION WORKS
- PUBLIC ACCESS
- STAFF ACCESS
- LOGISTIC ACCESS
- CONSTRUCTION TRUCK ACCESS

- GENERAL NOTE:

- PRELIMINARY ONLY. REFER TO MASTER SEQUENCING DIAGRAMS FOR MORE DETAILS
- TRAFFIC AND ROAD DESIGN TO BE PROVIDED BY SCT
- REFER TO NE BUILDING SET AND REFURB FOR DEMOLITION DETAIL SCOPE

RELOCATION OF
DEMOUNTABLE no.1 TO
WODONGA HOSPITAL.

RELOCATION OF
DEMOUNTABLE NO.2 TO
EAST SIDE OF EMERGENCY
DEPARTMENT.

MANAGED SITE
ACCESS DURING
CONSTRUCTION OF
NORTHEAST
BUILDING.


DELIVERY OF
INTEGRATED PROJECT
OFFICE

ENSURE EMERGENCY
DEPARTMENT ACCESS
REMAINS OPERATIONAL
THROUGHOUT THE
CONSTRUCTION PERIOD

SITE PREPARATION FOR
VERGE PARKING UNDER
REVIEW BY CIVIL TRAFFIC
AND LANDSCAPE TEAM
FOR THE SCOPE OF
DEMOLITION

ACCESS FOR
CONSTRUCTION FROM
THE EAST ROAD.
FEASIBILITY TO BE
REVIEWED BY SCT.

ISOMETRIC - STAGE 1

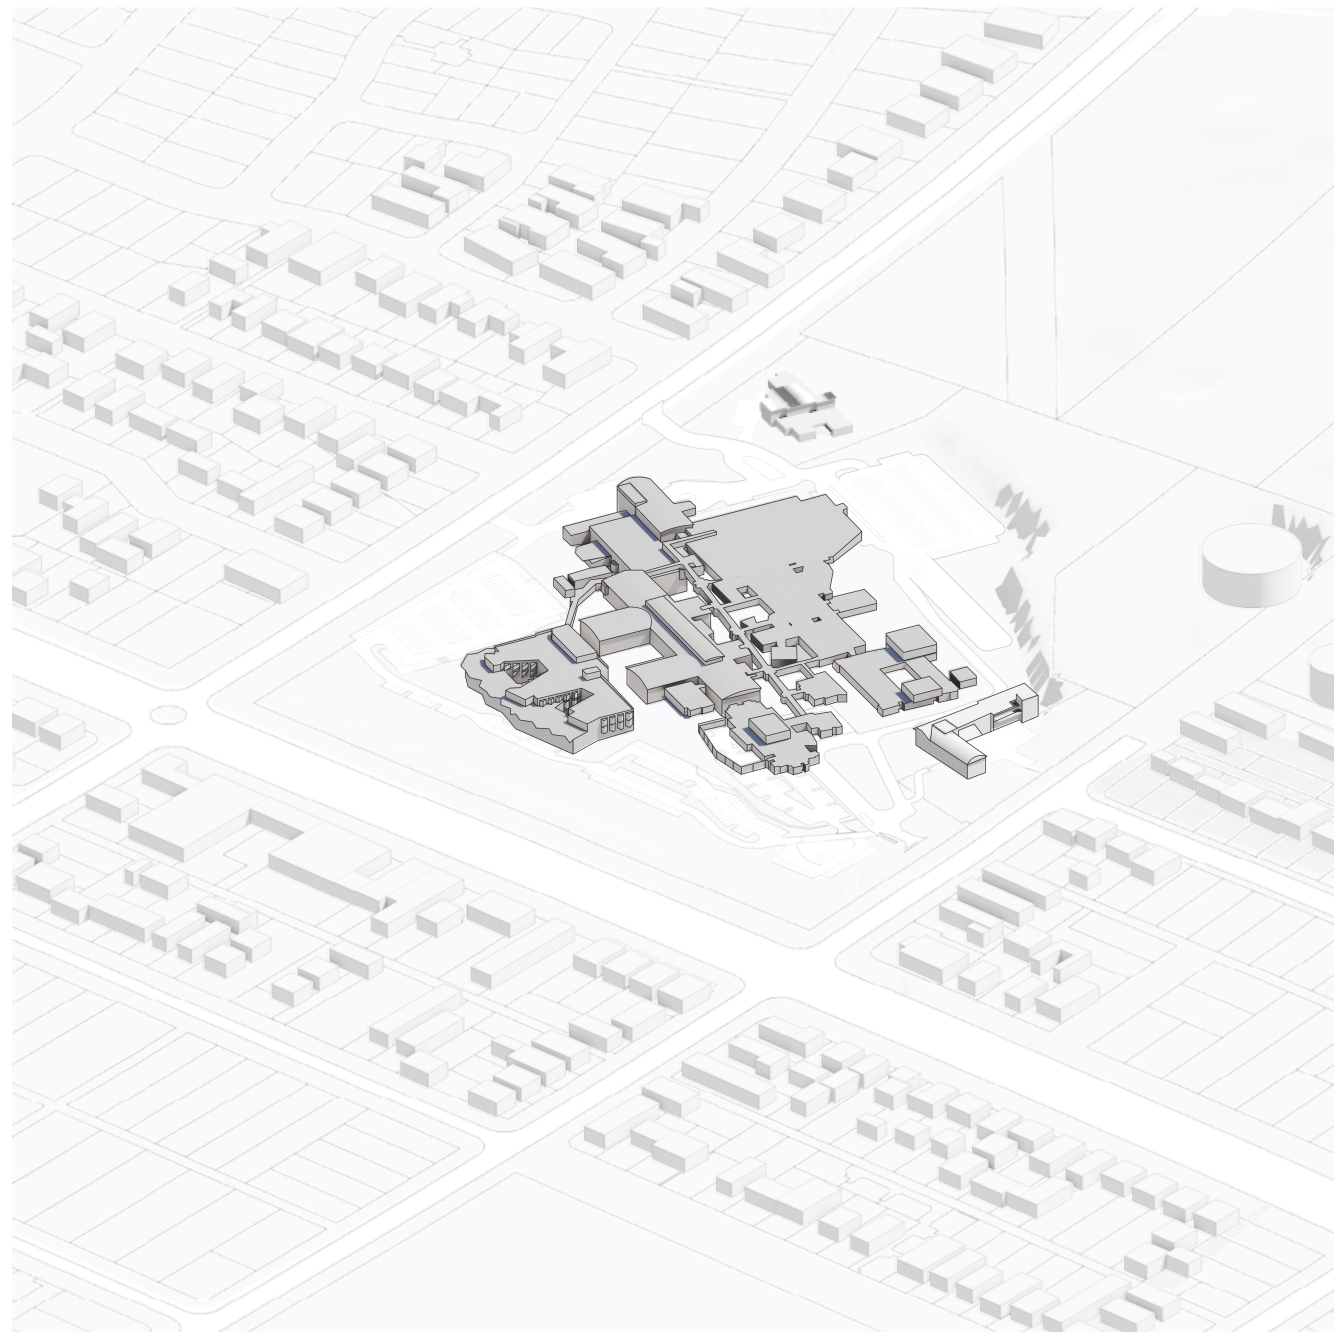

TEMPORARY
CARPARKING FOR NE
BUILDING.

HILL TOP
ACCOMODATION

EXISTING ALBURY HOSPITAL

UNSW RURAL
CLINICAL CAMPUS


PEECHELBA STREET

KEENE STREET

BORELLA ROAD

BILBA STREET

BENYON STREET

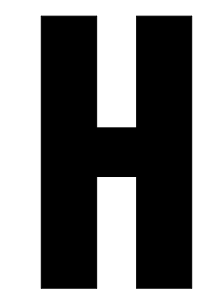


CONSULTANT

Hassell

Hassell LTD ABN 24 007 711 435
Level2, Pier 8/9,23 Hickson Rd
Sydney NSW 2000 Australia
T +61 2 9101 2000
F +61 2 9101 2100
sydney@hassellstudio.com
Nominated Architects NSW
Tony Grest 5330
Gerr Scott 5842
Ross de la Motte 7398

NORTH

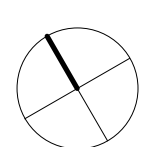

0m 1m 2m 3m 4m

NOTES

- Do not scale drawing. Written dimensions govern
 - All dimensions are in millimeters unless noted otherwise
 - All dimensions shall be verified on site before proceeding with the work. Hassell shall be notified in writing of any discrepancies.
 - This drawing must be read in conjunction with all relevant contracts, specifications and drawings.
- This drawing is an uncontrolled copy. Unless noted otherwise
© Copyright of this drawing is vested in Hassell Ltd.

REV DESCRIPTION

A SCHEMATIC DESIGN

DATE

19/12/2024

CLIENT

Health Infrastructure NSW

PROJECT

Albury Wodonga Regional Hospital
Project - CSB
201 Borella Road, East Albury

STATUS

SCHEMATIC DESIGN

DRAWING TITLE

STAGE 01 - ENABLING WORKS FOR
NE BUILDING

REVIEWED

CG

APPROVED

AS

DRAWING NO.
AWH-HSL-AR-MW-CSB-
00-DWG-XX103

SCALE @ A0

As Indicated

PROJECT NO.

016713

REV NO.

A