


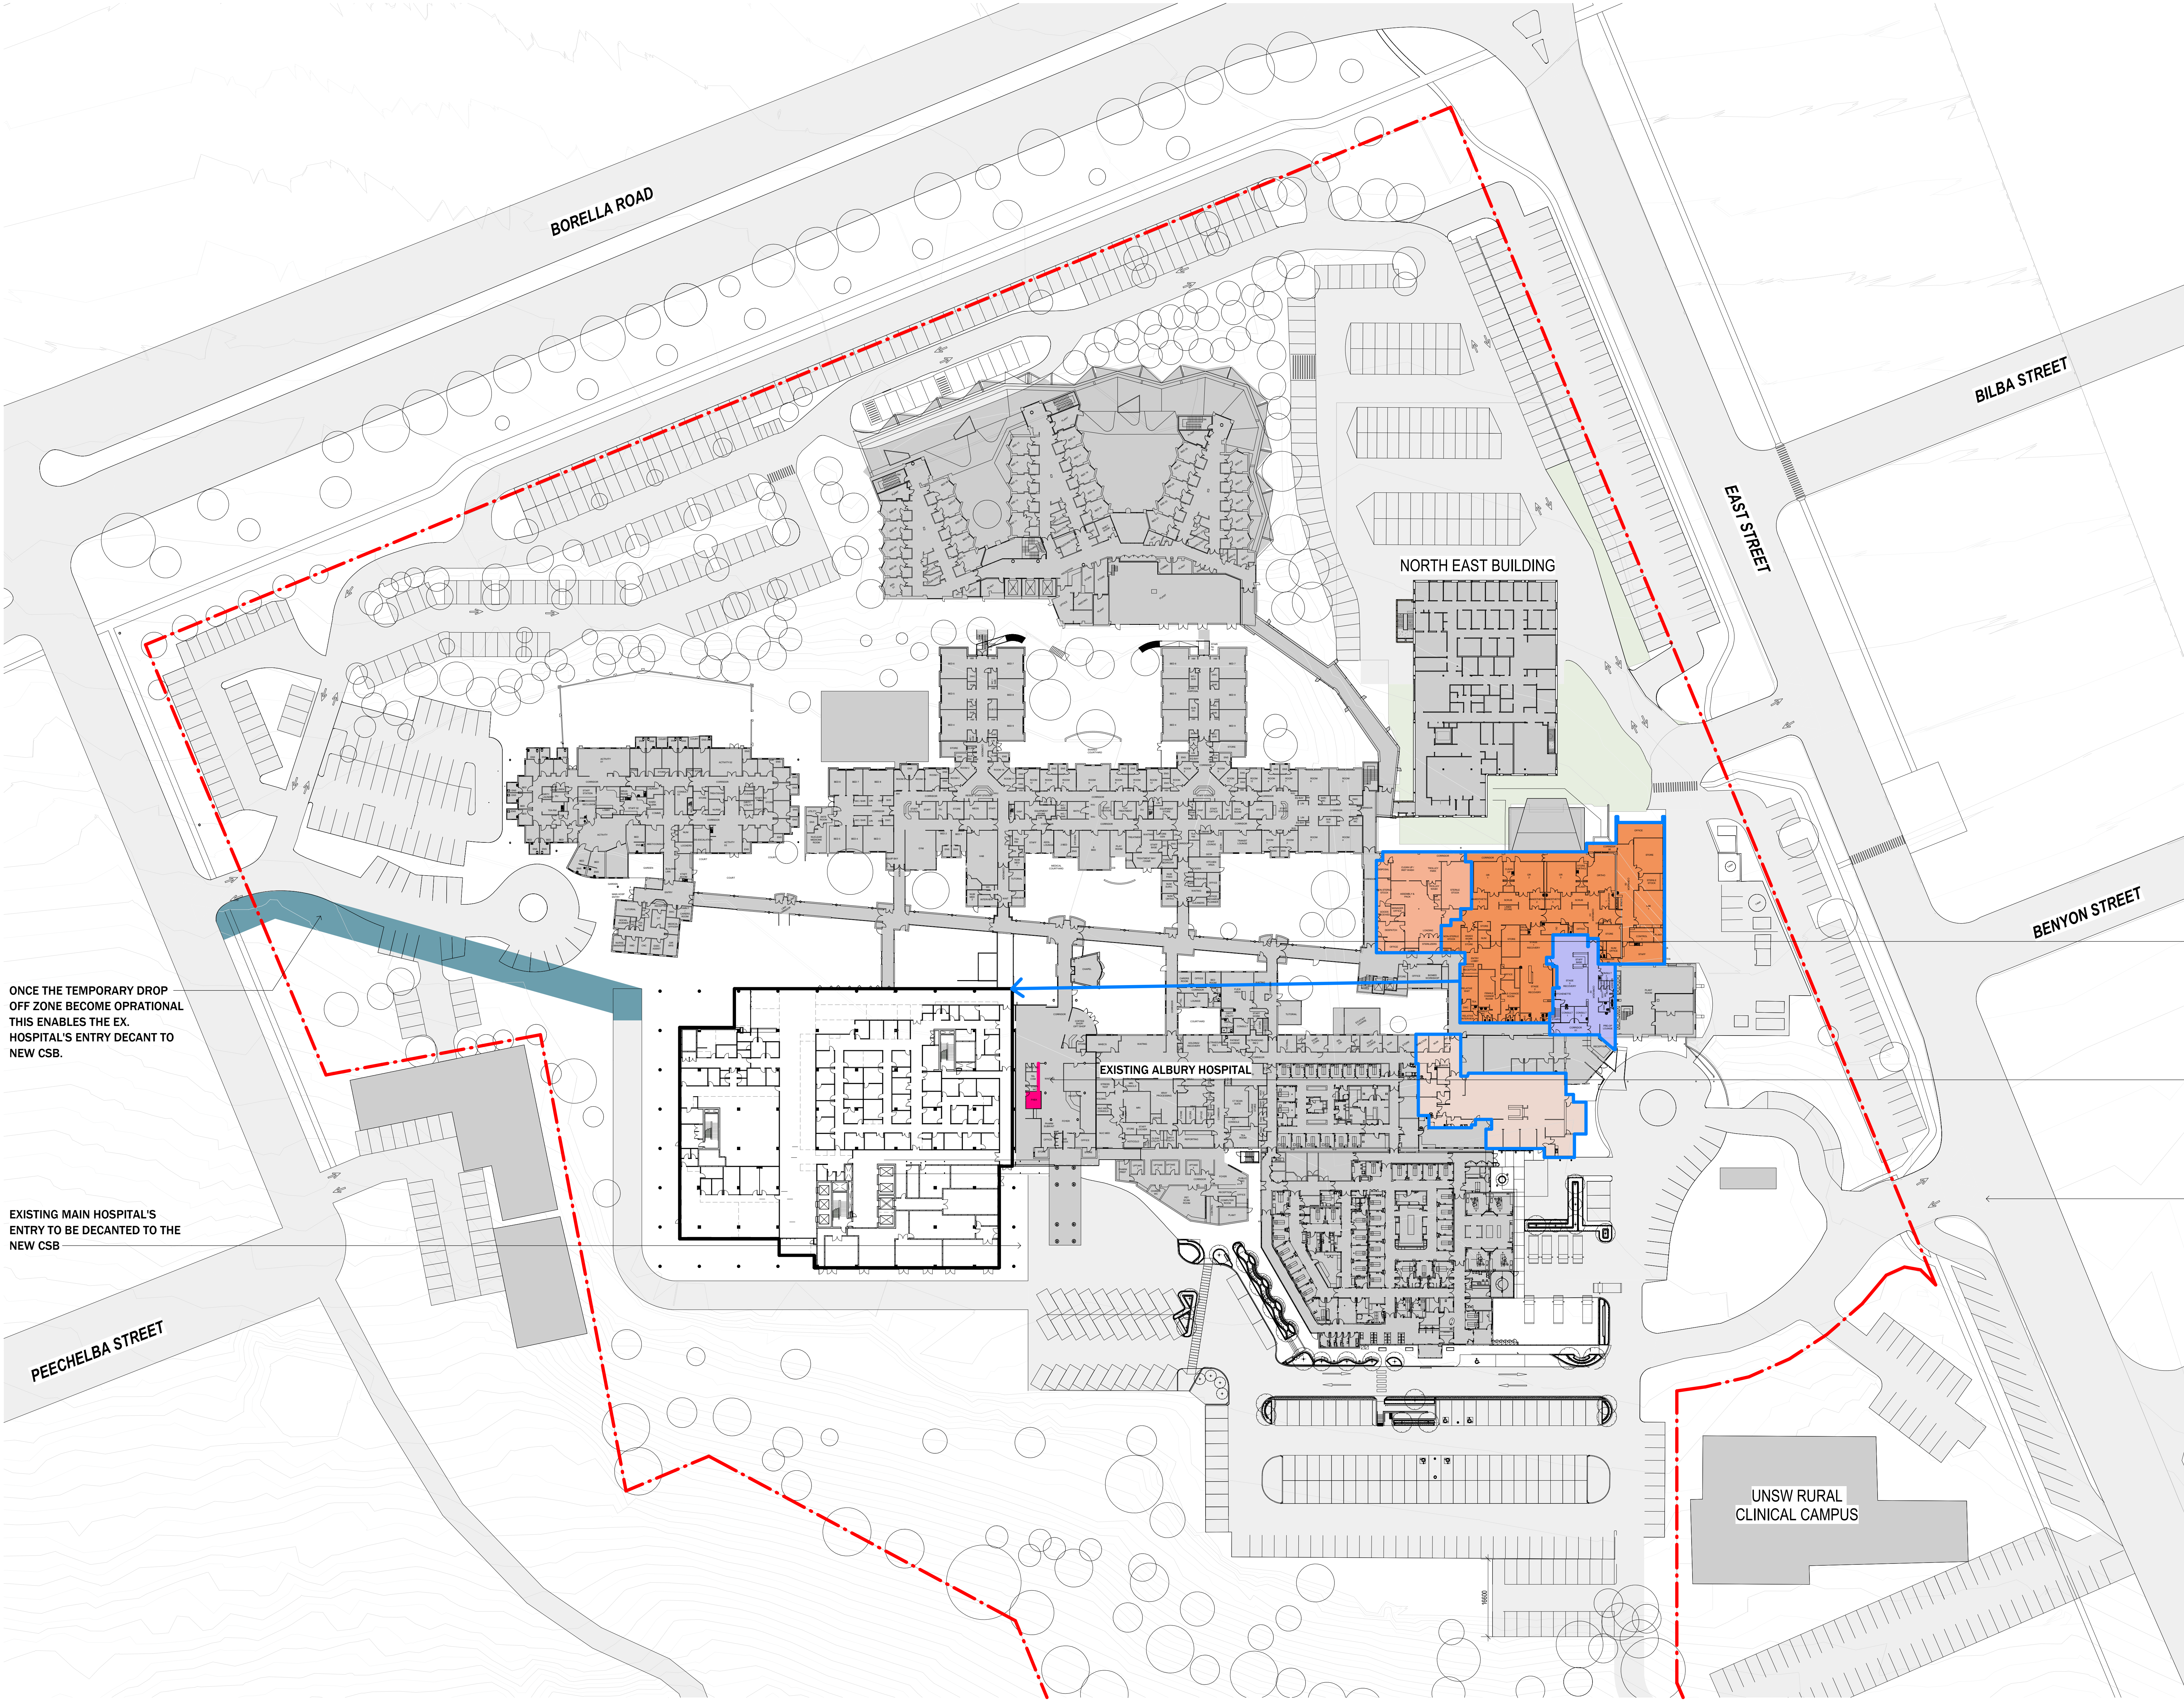

LEGEND:

- DEMOLITION / SITE PREPARATION
- TEMPORARY PARKING
- DECANT ON SITE
- DECANT OFF SITE
- NEW BUILD
- EXISTING
- PROTECTION WORKS
- PUBLIC ACCESS
- STAFF ACCESS
- LOGISTIC ACCESS
- CONSTRUCTION TRUCK ACCESS

- GENERAL NOTE:

- PRELIMINARY ONLY. REFER TO MASTER SEQUENCING DIAGRAMS FOR MORE DETAILS
- TRAFFIC AND ROAD DESIGN TO BE PROVIDED BY SCT
- REFER TO ME BUILDING SET AND REFURS FOR DEMOLITION DETAIL SCOPE

DEPARTMENT LEGEND:


- ALLIED HEALTH
- BIOMED WORKSHOP
- BREAST CANCER
- CARDIAC CLINIC
- CSSD
- DPU
- ETR
- EMERGENCY
- FOH
- IOU
- IPU MENTAL HEALTH
- MED IMAGING
- PATHOLOGY
- PATIENT SUPPORT
- PHARMACY
- PLANT
- THEATRE

PATIENTS, STAFF AND LOGISTIC ACCESS TO REMAIN FUNCTIONAL ALONG CENTRAL CORRIDOR

PABX ROOM TO BE PROTECTED DURING CONSTRUCTION. REFER TO INTERFACE DRAWINGS FOR MORE DETAILS . DN XXX

ED ACCESS TO REMAIN OPERATIONAL THROUGHOUT CONSTRUCTION

ISOMETRIC - STAGE 5

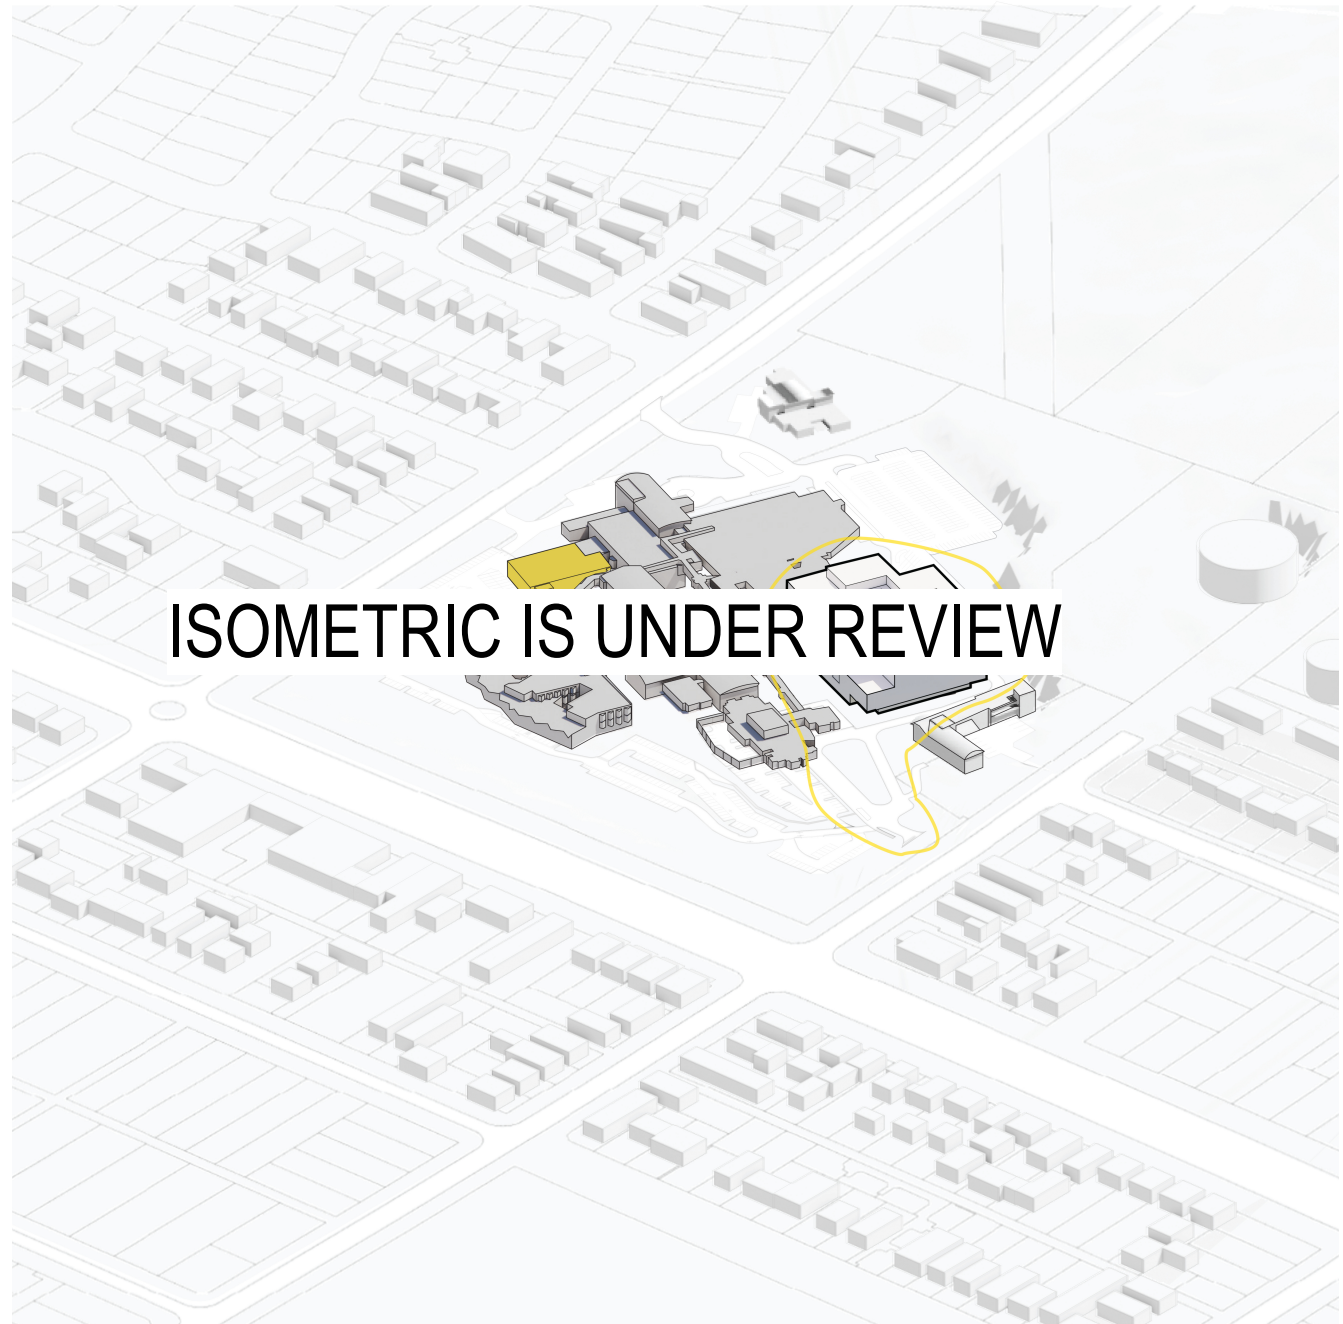

ONCE THE TEMPORARY DROP OFF ZONE BECOME OPERATIONAL THIS ENABLES THE EX. HOSPITAL'S ENTRY DECANT TO NEW CSB.


EXISTING MAIN HOSPITAL'S ENTRY TO BE DECANTED TO THE NEW CSB

CONSULTANT

Hassell

Hassell LTD ABN 24 007 711 435
Level2, Pier 8/9,23 Hickson Rd
Sydney NSW 2000 Australia
T +61 2 9101 2000
F +61 2 9101 2100
sydney@hassellstudio.com
Nominated Architects NSW
Tony Grant 0300
Gerr Scott 0842
Ross de la Motte 7398

NORTH

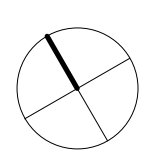

0m 1m 2m 3m 4m

NOTES

- Do not scale drawing. Written dimensions govern
 - All dimensions are in millimeters unless noted otherwise
 - All dimensions shall be verified on site before proceeding with the work. Hassell shall be notified in writing of any discrepancies.
 - This drawing must be read in conjunction with all relevant contracts, specifications and drawings.
- This drawing is an uncontrolled copy. Unless noted otherwise
© Copyright of this drawing is vested in Hassell Ltd.

REV DESCRIPTION

A SCHEMATIC DESIGN

DATE

19/12/2024

CLIENT

Health Infrastructure NSW

PROJECT

Albury Wodonga Regional Hospital
Project - CSB
201 Borella Road, East Albury

STATUS

SCHEMATIC DESIGN

DRAWING TITLE

STAGE 05 - DECANT TO CSB

REVIEWED

CG

APPROVED

AS

DRAWING NO.
AWH-HSL-AR-MW-CSB-
00-DWG-XX107

SCALE @ A0

As Indicated

PROJECT NO.

016713

REV NO.

A