


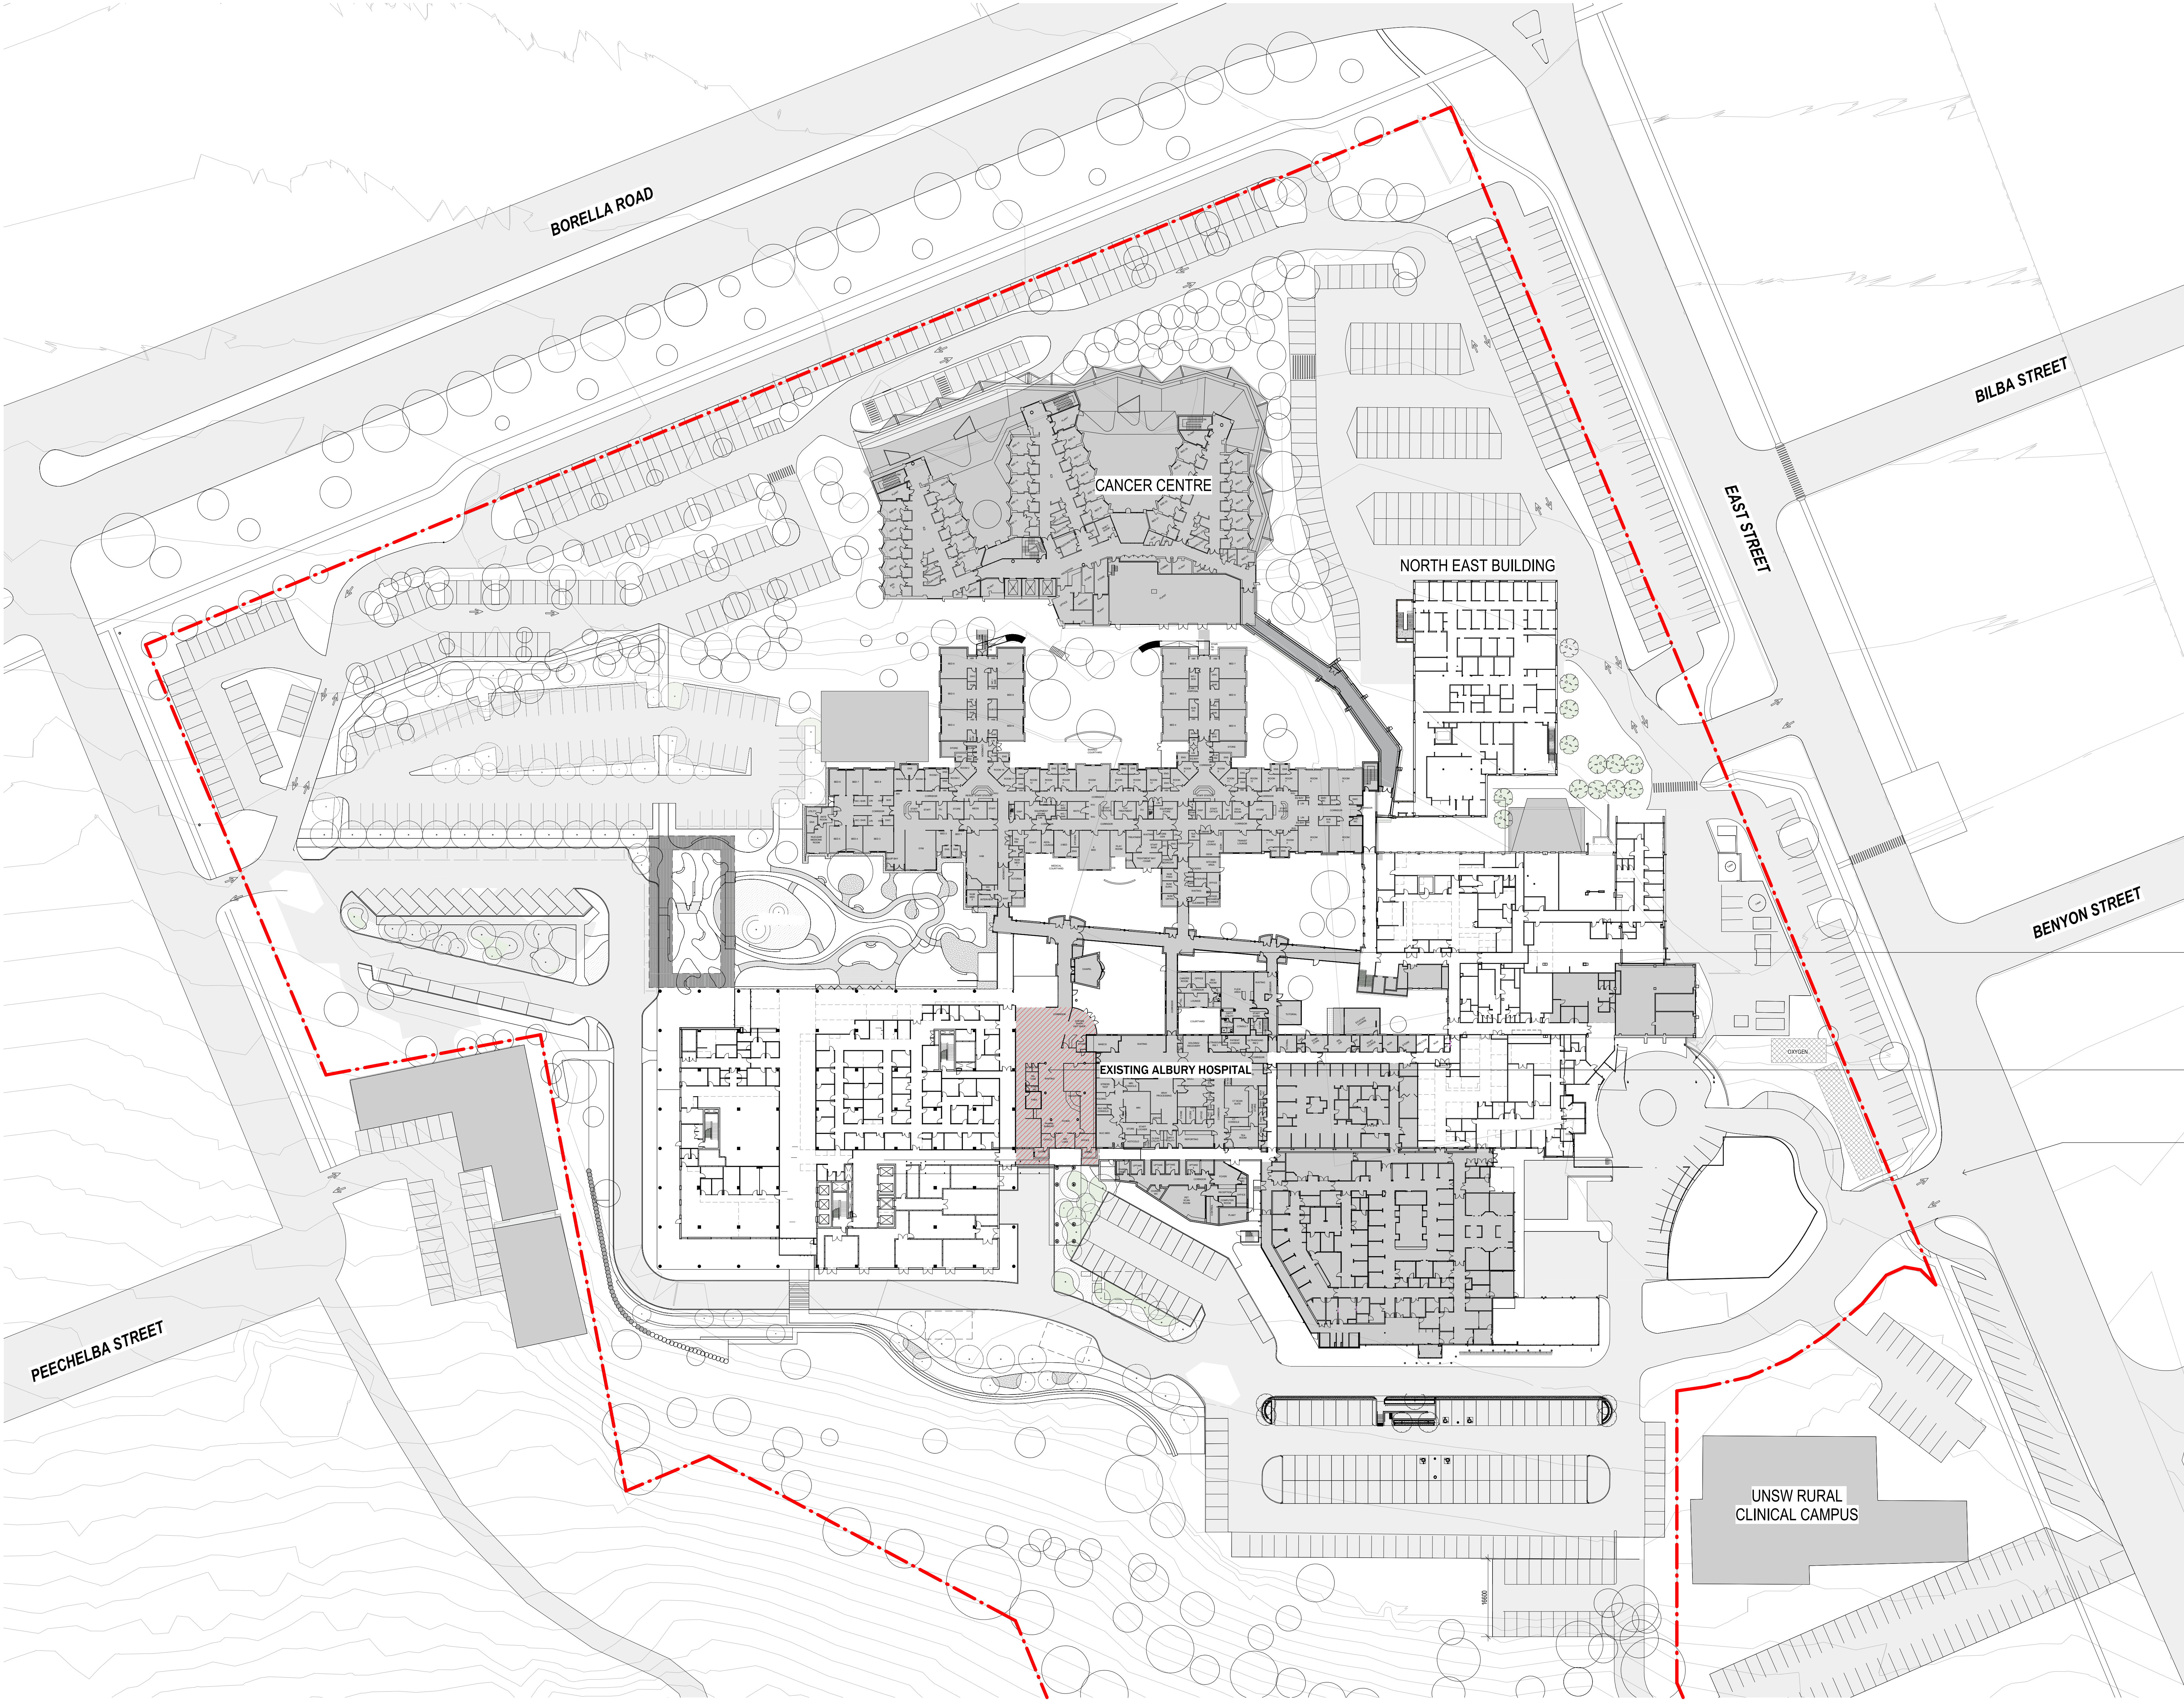

LEGEND:

- DEMOLITION / SITE PREPARATION
- TEMPORARY PARKING
- DECANT ON SITE
- DECANT OFF SITE
- NEW BUILD
- EXISTING
- PROTECTION WORKS
- PUBLIC ACCESS
- STAFF ACCESS
- LOGISTIC ACCESS
- CONSTRUCTION TRUCK ACCESS

- GENERAL NOTE:

- PRELIMINARY ONLY. REFER TO MASTER SEQUENCING DIAGRAMS FOR MORE DETAILS
- TRAFFIC AND ROAD DESIGN TO BE PROVIDED BY SCT
- REFER TO THE BUILDING SET AND REFURS FOR DEMOLITION DETAIL SCOPE

DEPARTMENT LEGEND:



- ALLIED HEALTH
- BIOMED WORKSHOP
- BREAST CANCER
- CARDIAC CLINIC
- CSSD
- DPU
- ETR
- EMERGENCY
- FOH
- IOU
- IPU MENTAL HEALTH
- MED IMAGING
- PATHOLOGY
- PATIENT SUPPORT
- PHARMACY
- PLANT
- THEATRE

PATIENTS, STAFF AND LOGISTICS ACCESS TO REMAIN FUNCTIONAL ALONG THE CENTRAL CORRIDOR

EXISTING FOH TO BE DEMOLISHED

ED ACCESS TO REMAIN OPERATIONAL THROUGHOUT CONSTRUCTION

ISOMETRIC - STAGE 7

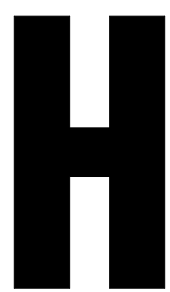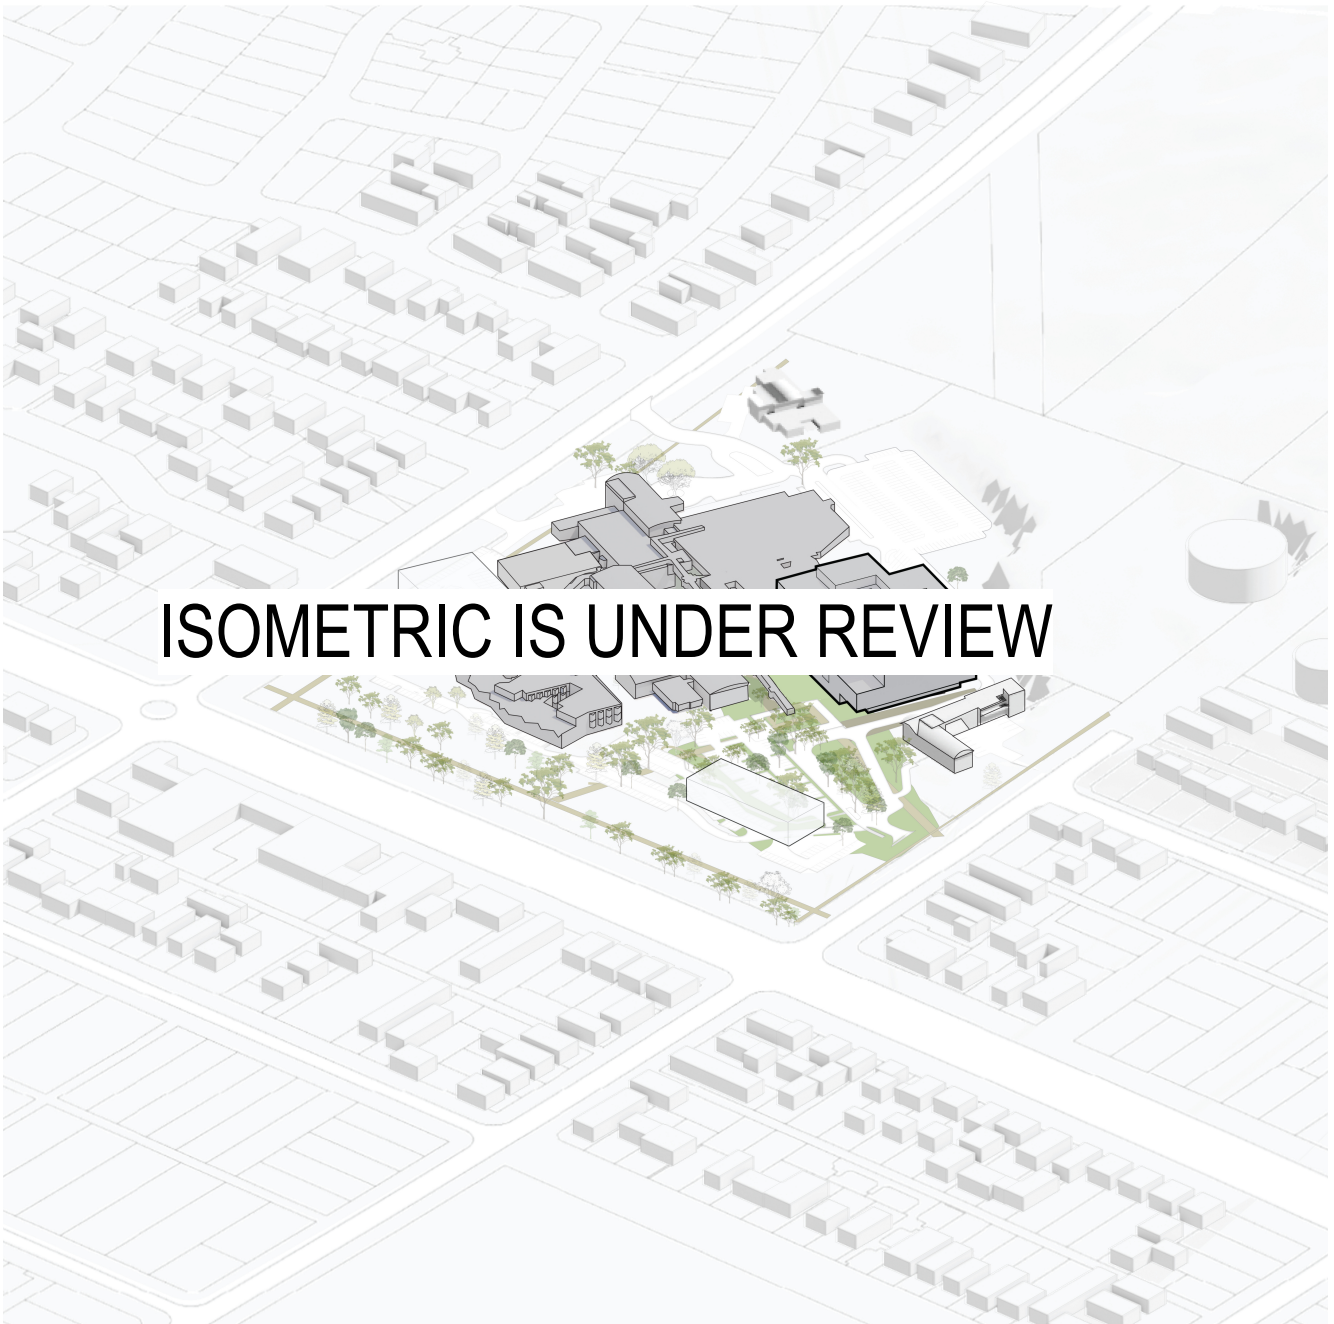


CONSULTANT

Hassell

Hassell LTD ABN 24 007 711 435
Level2, Pier 8/9,23 Hickson Rd
Sydney NSW 2000 Australia
T +61 2 9101 2000
F +61 2 9101 2100
sydney@hassellstudio.com
Nominated Architects NSW
Tony Grant 0330
Glen Scott 0842
Ross de la Motte 7398

NORTH

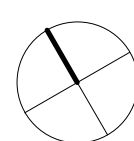

0m 1m 2m 3m 4m

NOTES

- Do not scale drawing. Written dimensions govern
 - All dimensions are in millimeters unless noted otherwise
 - All dimensions shall be verified on site before proceeding with the work. Hassell shall be notified in writing of any discrepancies.
 - This drawing must be read in conjunction with all relevant contracts, specifications and drawings
- This drawing is an uncontrolled copy. Unless noted otherwise
© Copyright of this drawing is vested in Hassell Ltd.

REV DESCRIPTION

A SCHEMATIC DESIGN

DATE

19/12/2024

CLIENT

Health Infrastructure NSW

PROJECT

Albury Wodonga Regional Hospital
Project - CSB
201 Borella Road, East Albury

STATUS

SCHEMATIC DESIGN

DRAWING TITLE

STAGE 07 - EX ENTRY DECANT

REVIEWED

CG

APPROVED

AS

DRAWING NO.
AWH-HSL-AR-MW-CSB-
00-DWG-XX109

SCALE @ A0

As Indicated

PROJECT NO.

016713

REV NO.

A