




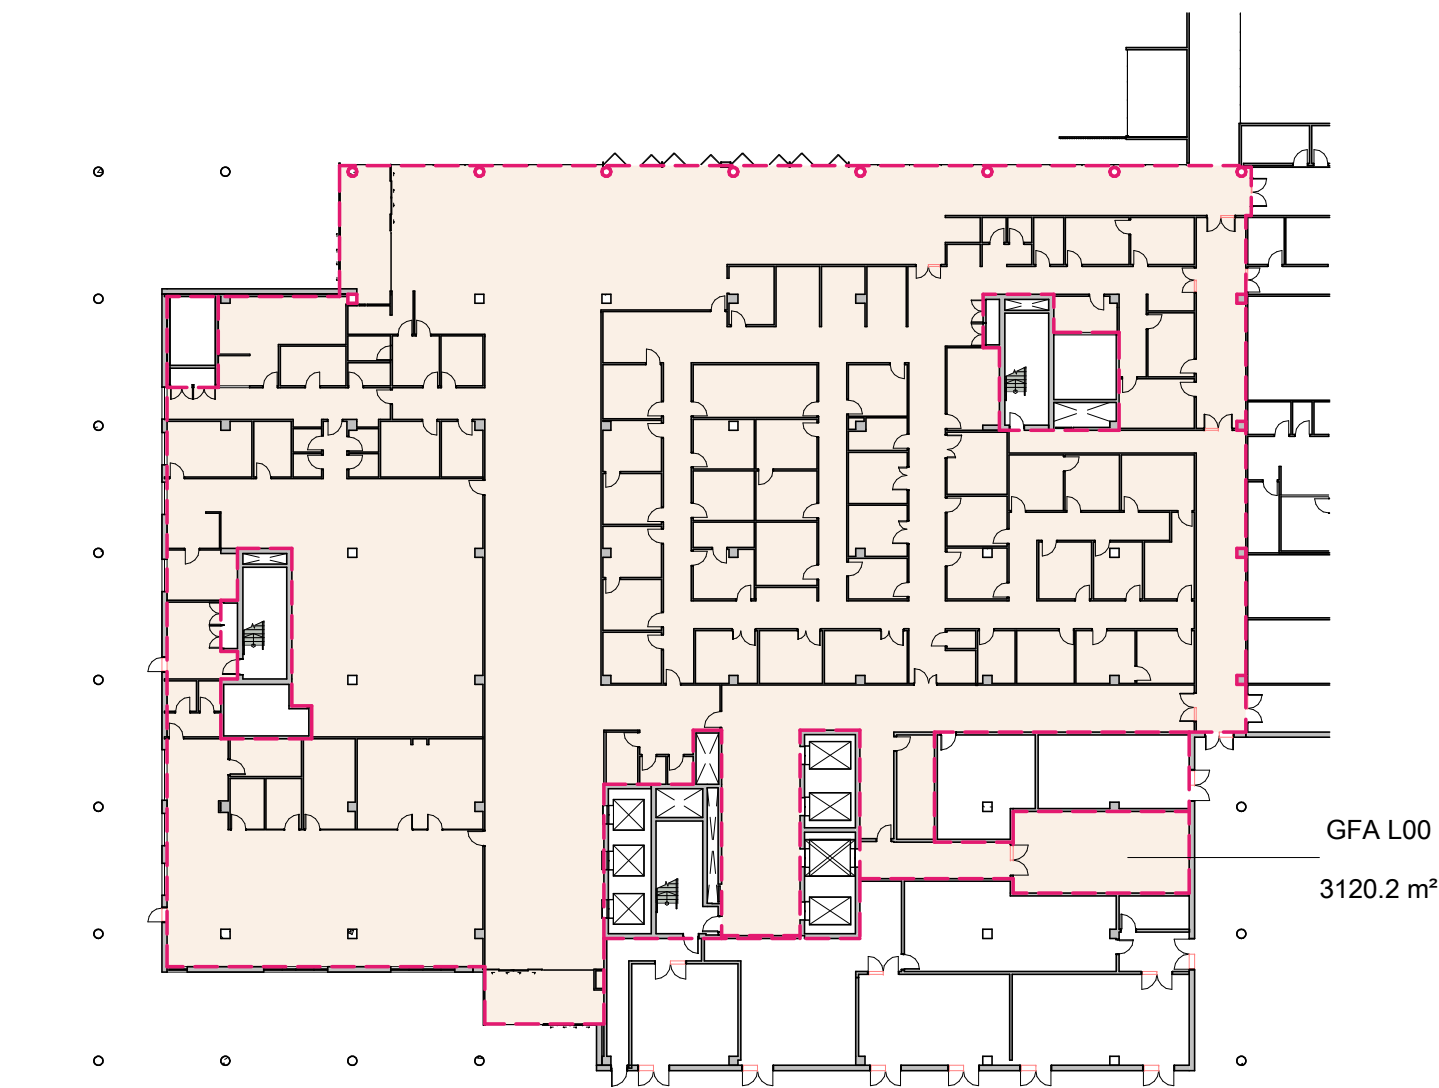


AREA PLAN - L02

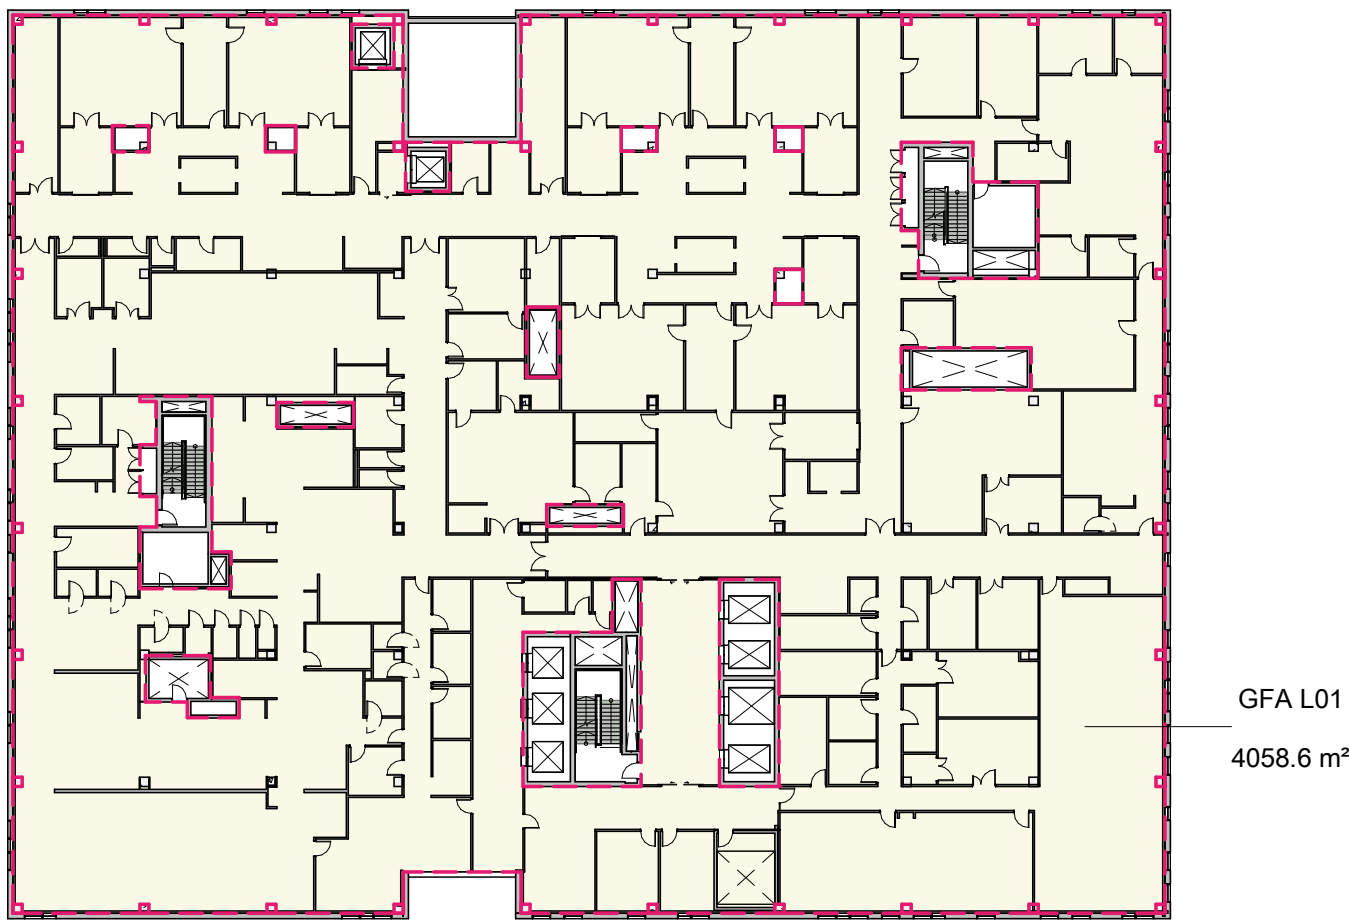


AREA PLAN - L03

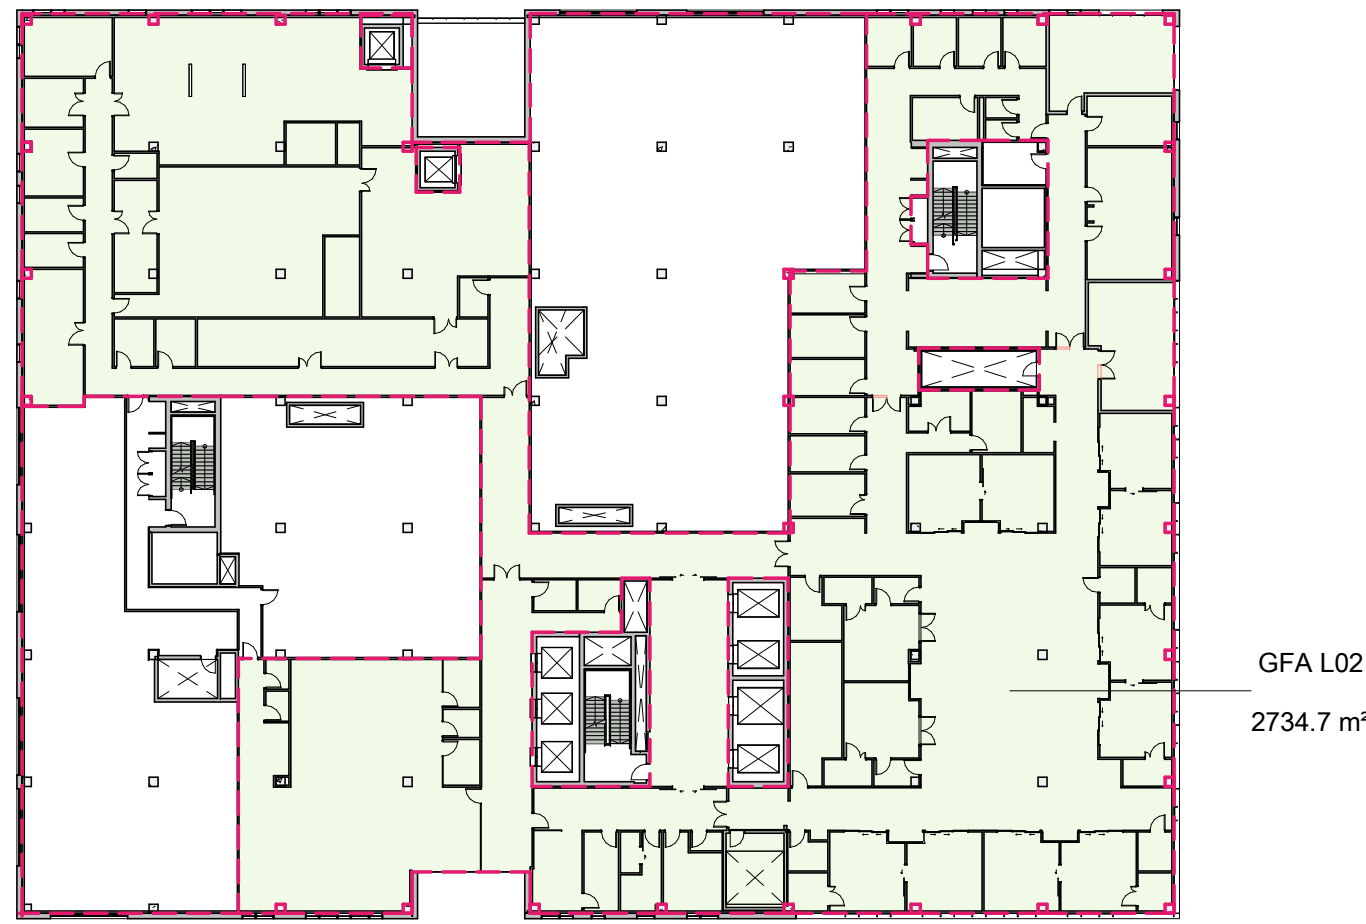


AREA PLAN - L04

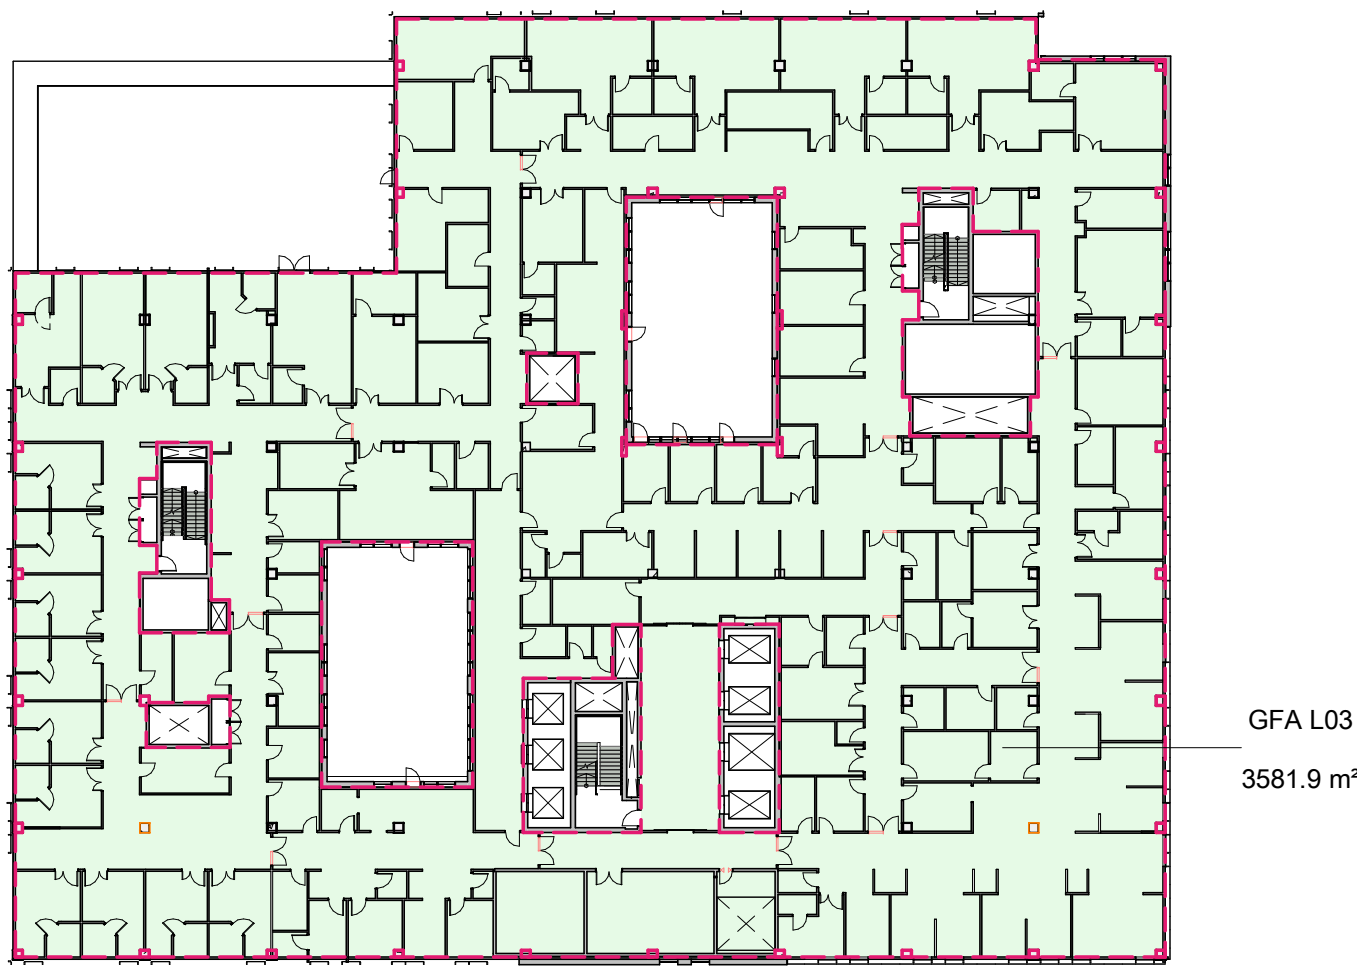


AREA PLAN - L05

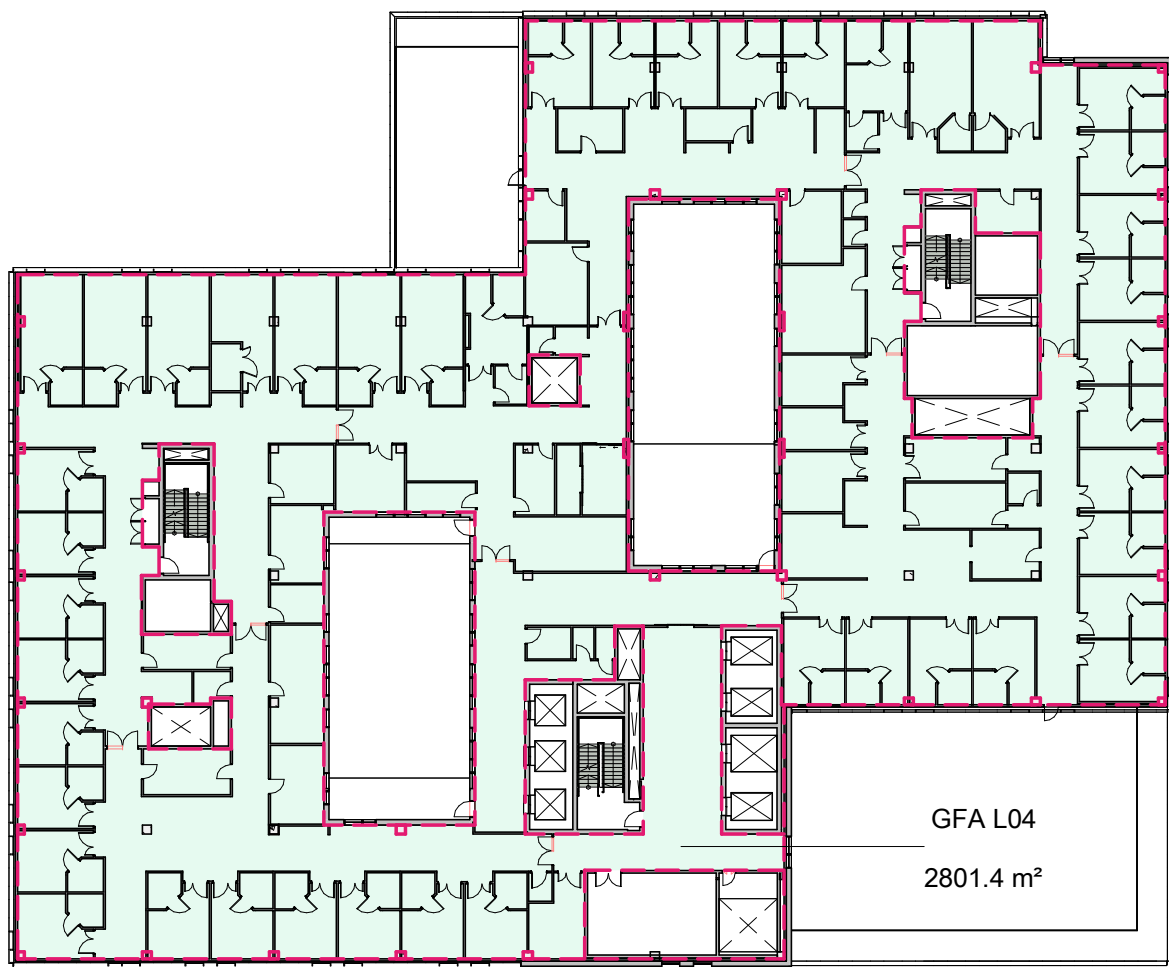


AREA PLAN - L06

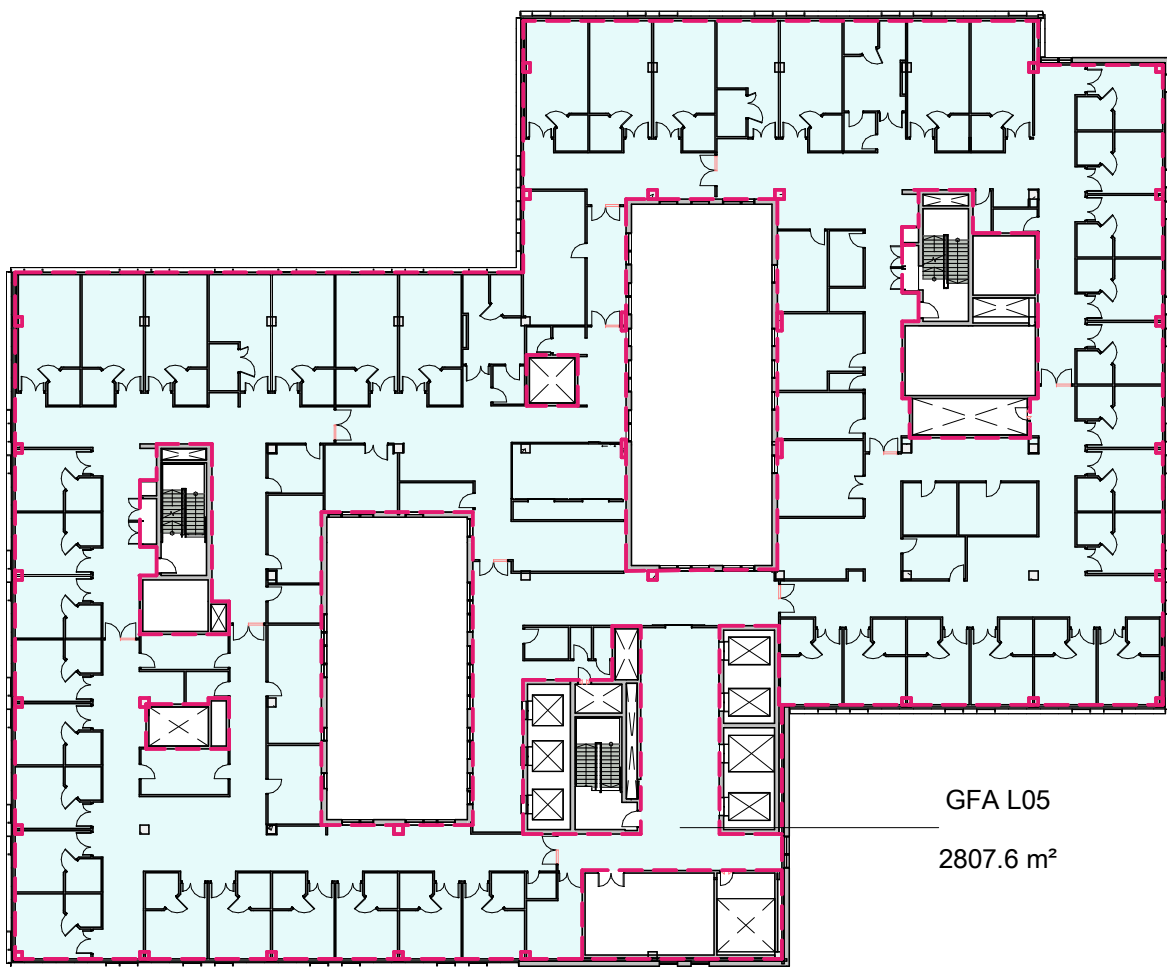

AREA PLAN - L07

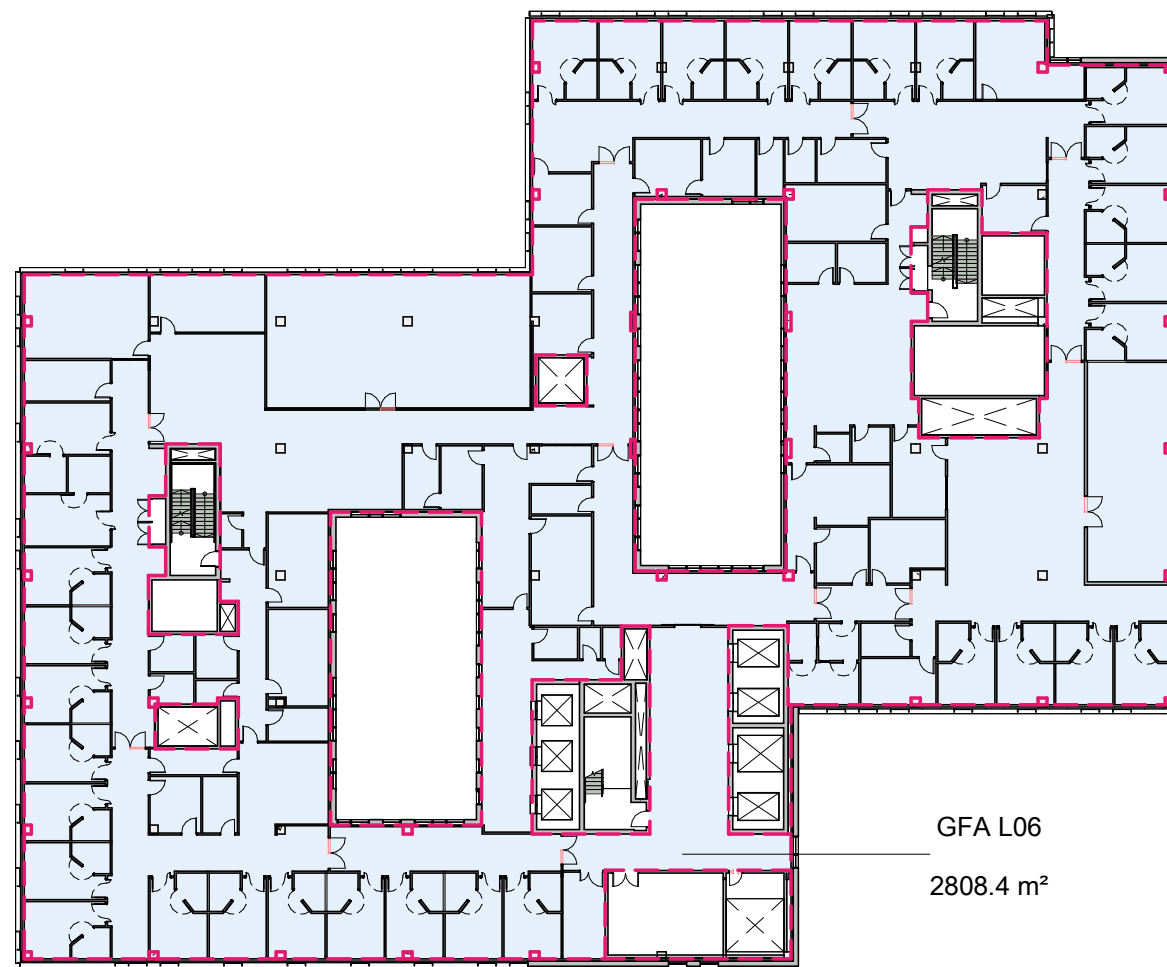


AREA PLAN - L08

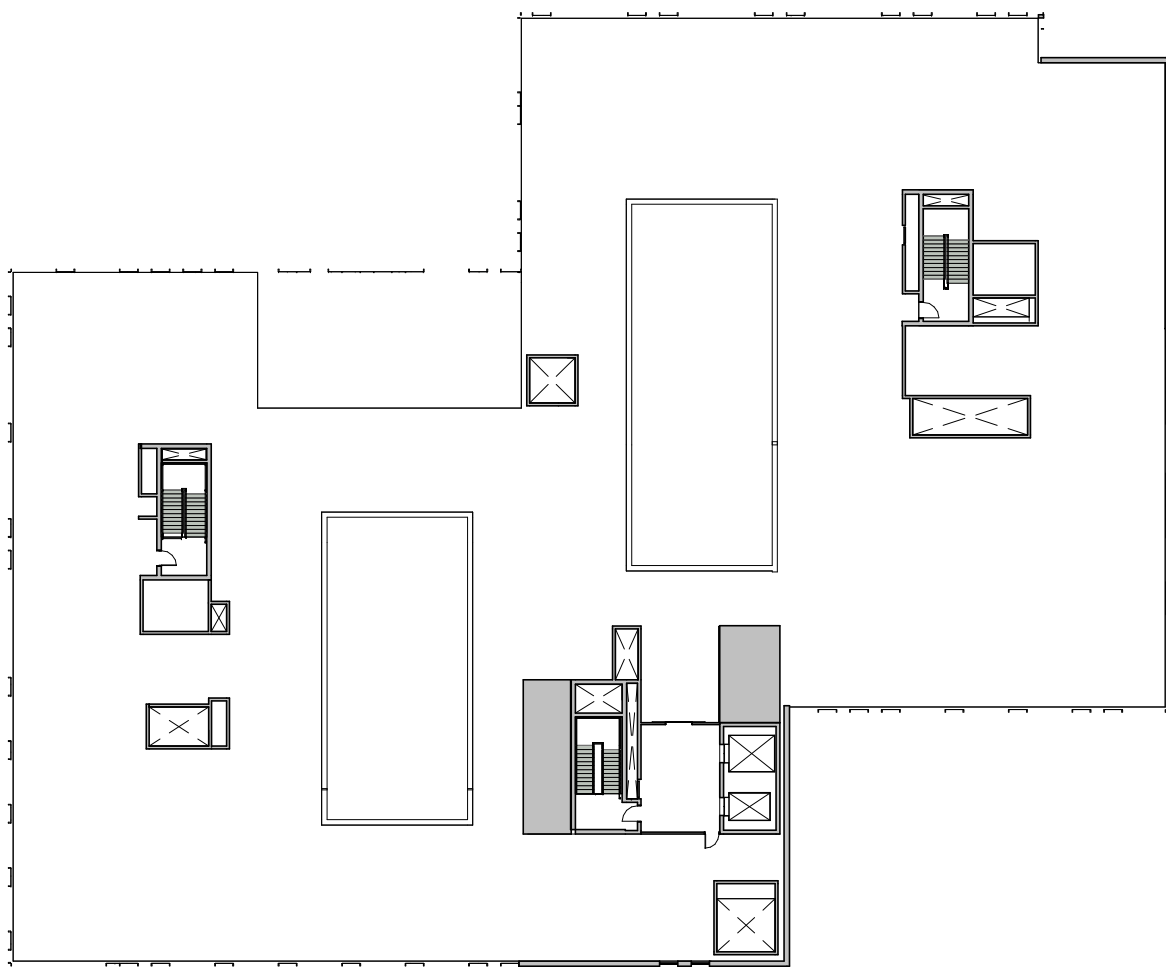

ROOF

Area Schedule (AREA_GFA)	
LEVEL	AREA
L02	3120 m²
L03	4059 m²
L04	2735 m²
L05	3582 m²
L06	2801 m²
L07	2808 m²
L08	2808 m²
	21913 m²

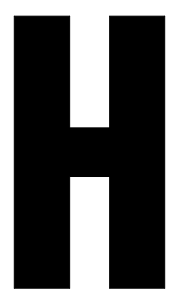


CONSULTANT

Hassell

Hassell LTD ABN 24 007 711 435
Level2, Pier 8/9,23 Hickson Rd
Sydney NSW 2000 Australia
T +61 2 9101 2000
F +61 2 9101 2100
sydney@hassellstudio.com
Nominated Architects NSW
Tony Grant 0330
Gerrit Scott 0842
Ross de la Motte 7398

NORTH

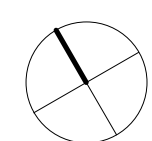

0m 5m 10m 15m 20m

NOTES

1. Do not scale drawing. Written dimensions govern
 2. All dimensions are in millimeters unless noted otherwise
 3. All dimensions shall be verified on site before proceeding with the work. Hassell shall be notified in writing of any discrepancies.
 4. This drawing must be read in conjunction with all relevant contracts, specifications and drawings.
- This drawing is an uncontrolled copy. Unless noted otherwise
© Copyright of this drawing is vested in Hassell Ltd.

REV DESCRIPTION

A SCHEMATIC DESIGN

DATE

19/12/2024

CLIENT

Health Infrastructure NSW

PROJECT

Albury Wodonga Regional Hospital
Project - CSB
201 Borella Road, East Albury

STATUS

SCHEMATIC DESIGN

DRAWING TITLE

GFA AREA PLANS

REVIEWED

AS

APPROVED

CL

DRAWING NO.
AWH-HSL-AR-MW-CSB-
01-DWG-XX001

SCALE @ A0

1 : 500

PROJECT NO.

016713

REV NO.

A