
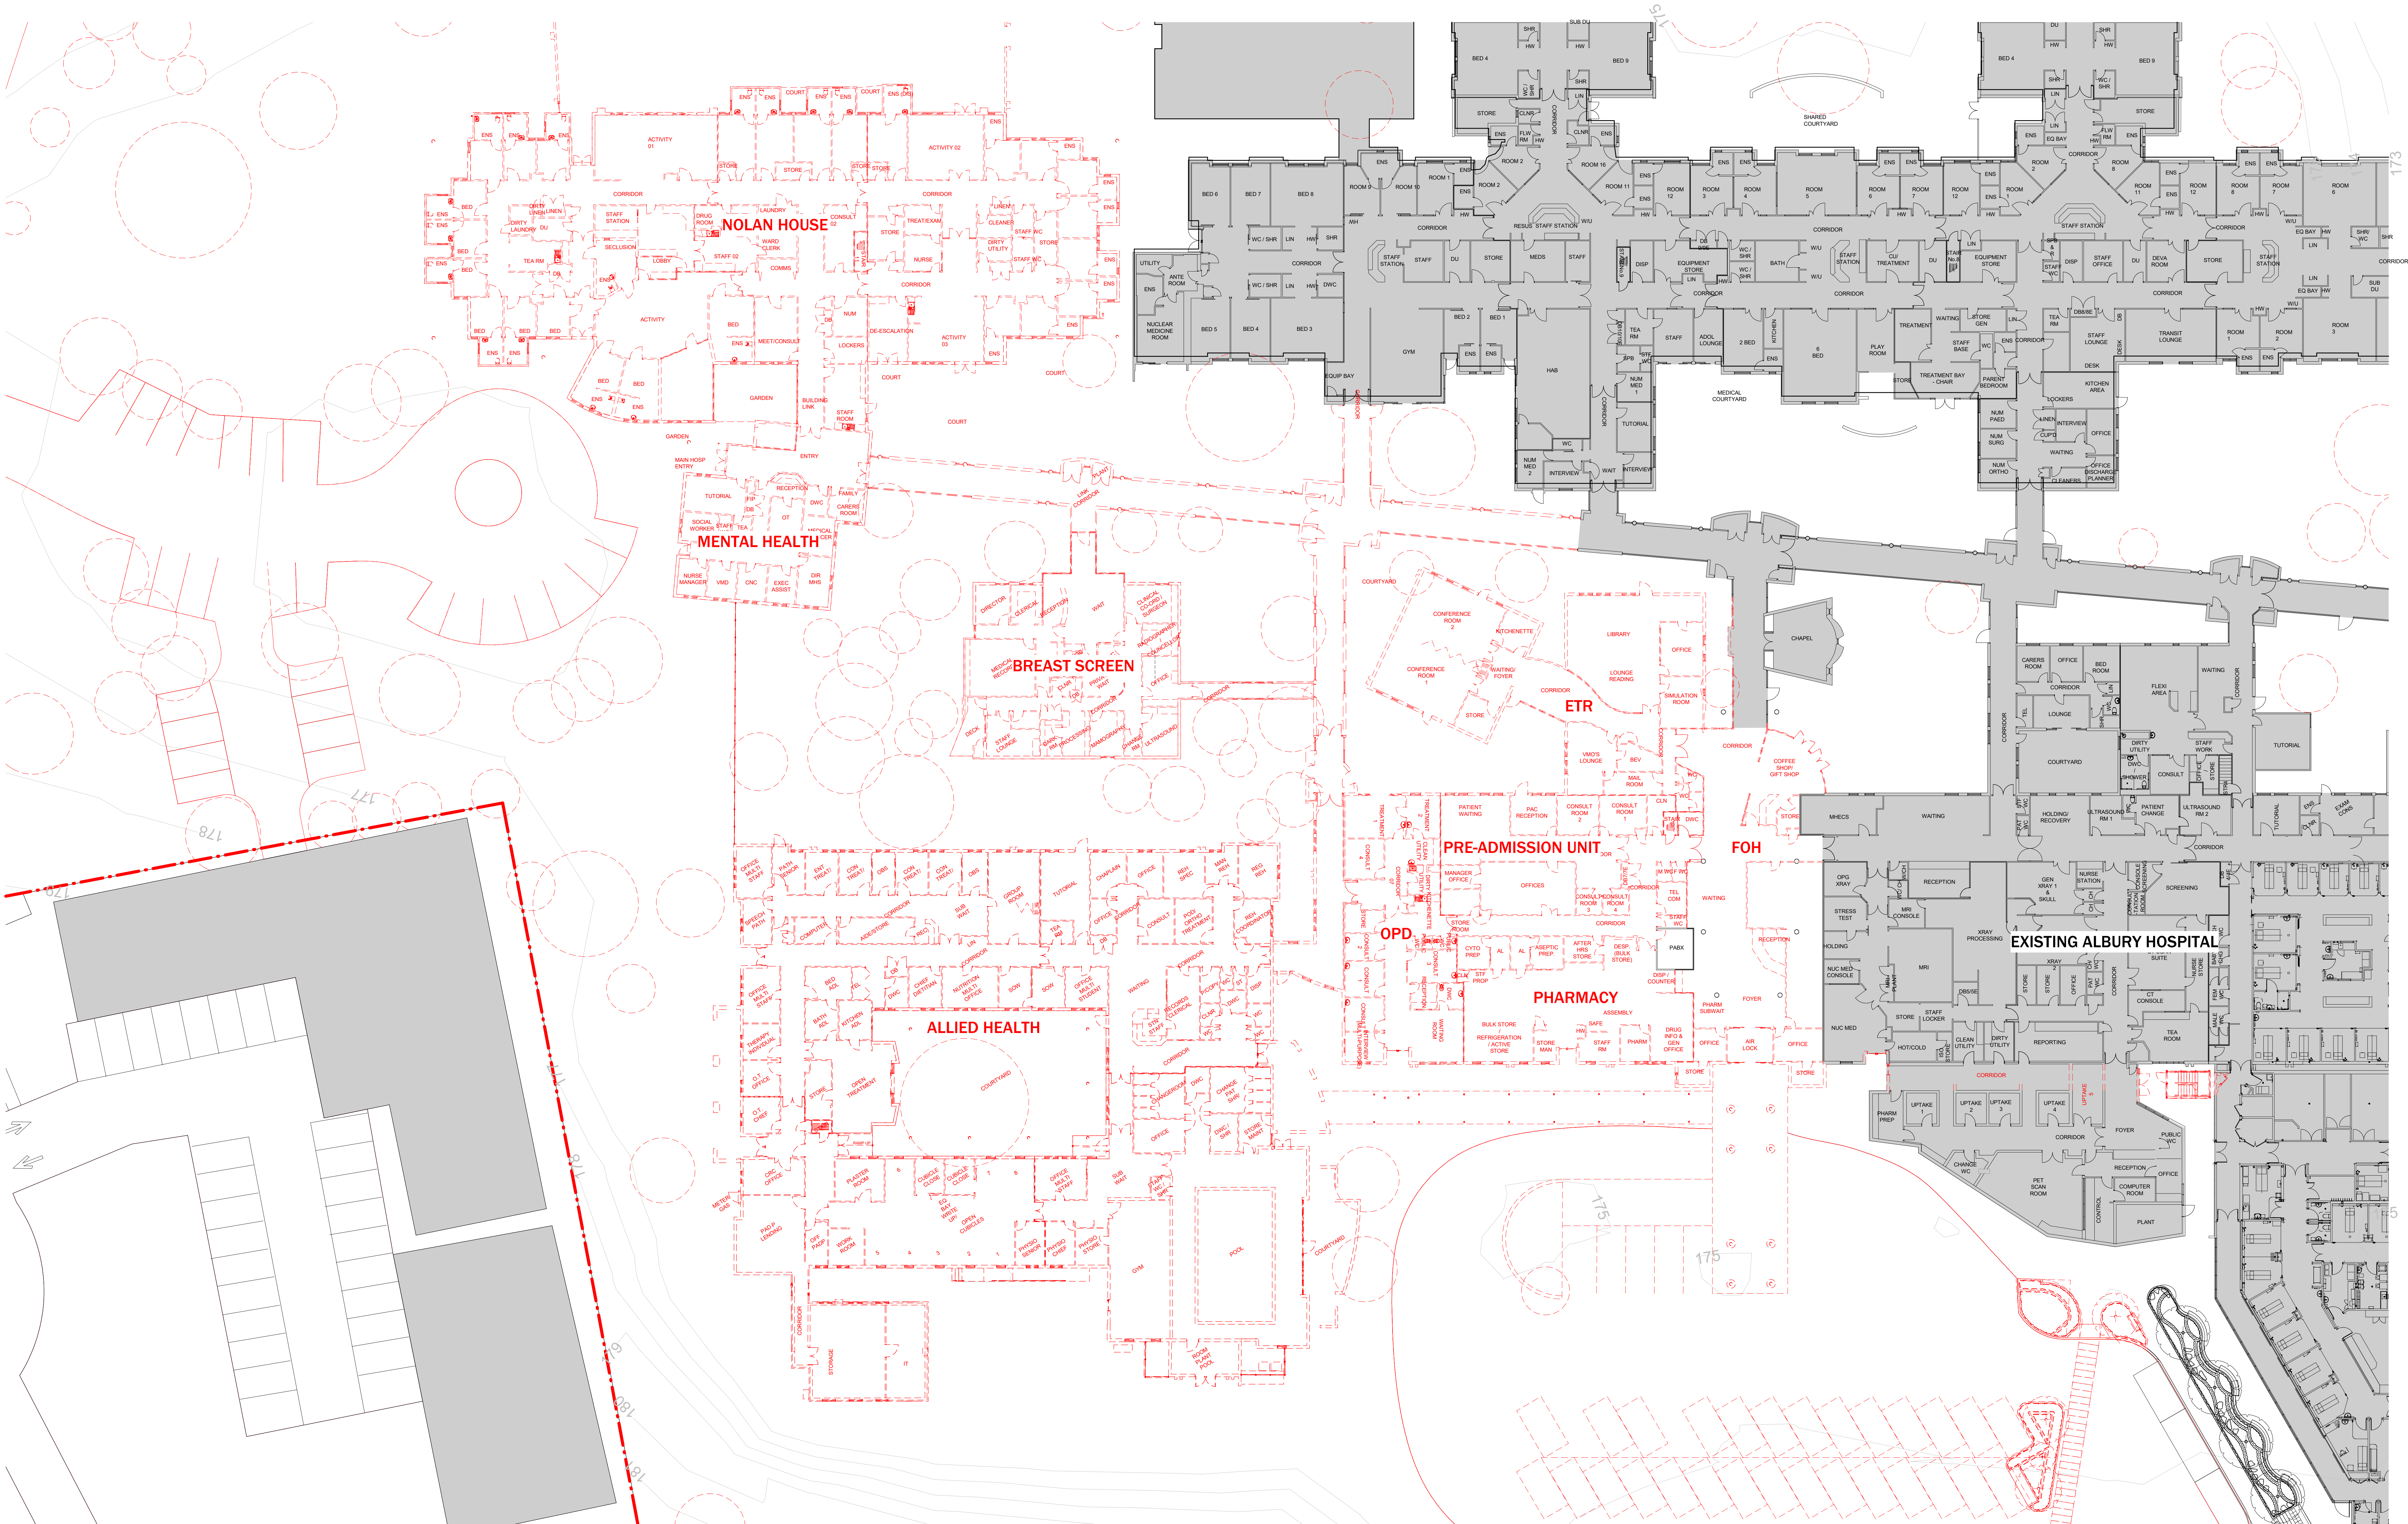


CONSULTANT

Hassell

Hassell LTD ABN 24 007 711 435
Level2, Pier 8/9/23 Hickson Rd
Sydney NSW 2000 Australia
T +61 2 9101 2000
F +61 2 9101 2100
sydney@hassellstudio.com
Nominated Architects NSW
Tony Grant 5330
Glen Scott 0842
Ross de la Motte 7398

NORTH

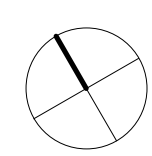

0m 1m 2m 3m 4m

NOTES

1. Do not scale drawing. Written dimensions govern
2. All dimensions are in millimeters unless noted otherwise
3. All dimensions shall be verified on site before proceeding with the work. Hassell shall be notified in writing of any discrepancies.
4. This drawing must be read in conjunction with all relevant contracts, specifications and drawings.

This drawing is an uncontrolled copy. Unless noted otherwise
© Copyright of this drawing is vested in Hassell Ltd.

REV DESCRIPTION

A SCHEMATIC DESIGN

DATE

19/12/2024

CLIENT

Health Infrastructure NSW

PROJECT

Albury Wodonga Regional Hospital
Project - CSB
201 Borella Road, East Albury

STATUS

DRAWING TITLE
DEMOLITION + TEMPORARY WORK
PLAN - LEVEL 2

REVIEWED
AS

APPROVED
CL

DRAWING NO.
AWH-HSL-AR-MW-CSB-
02-DWG-02001

SCALE @ A0
1 : 200

PROJECT NO.
016713

REV NO.
A