


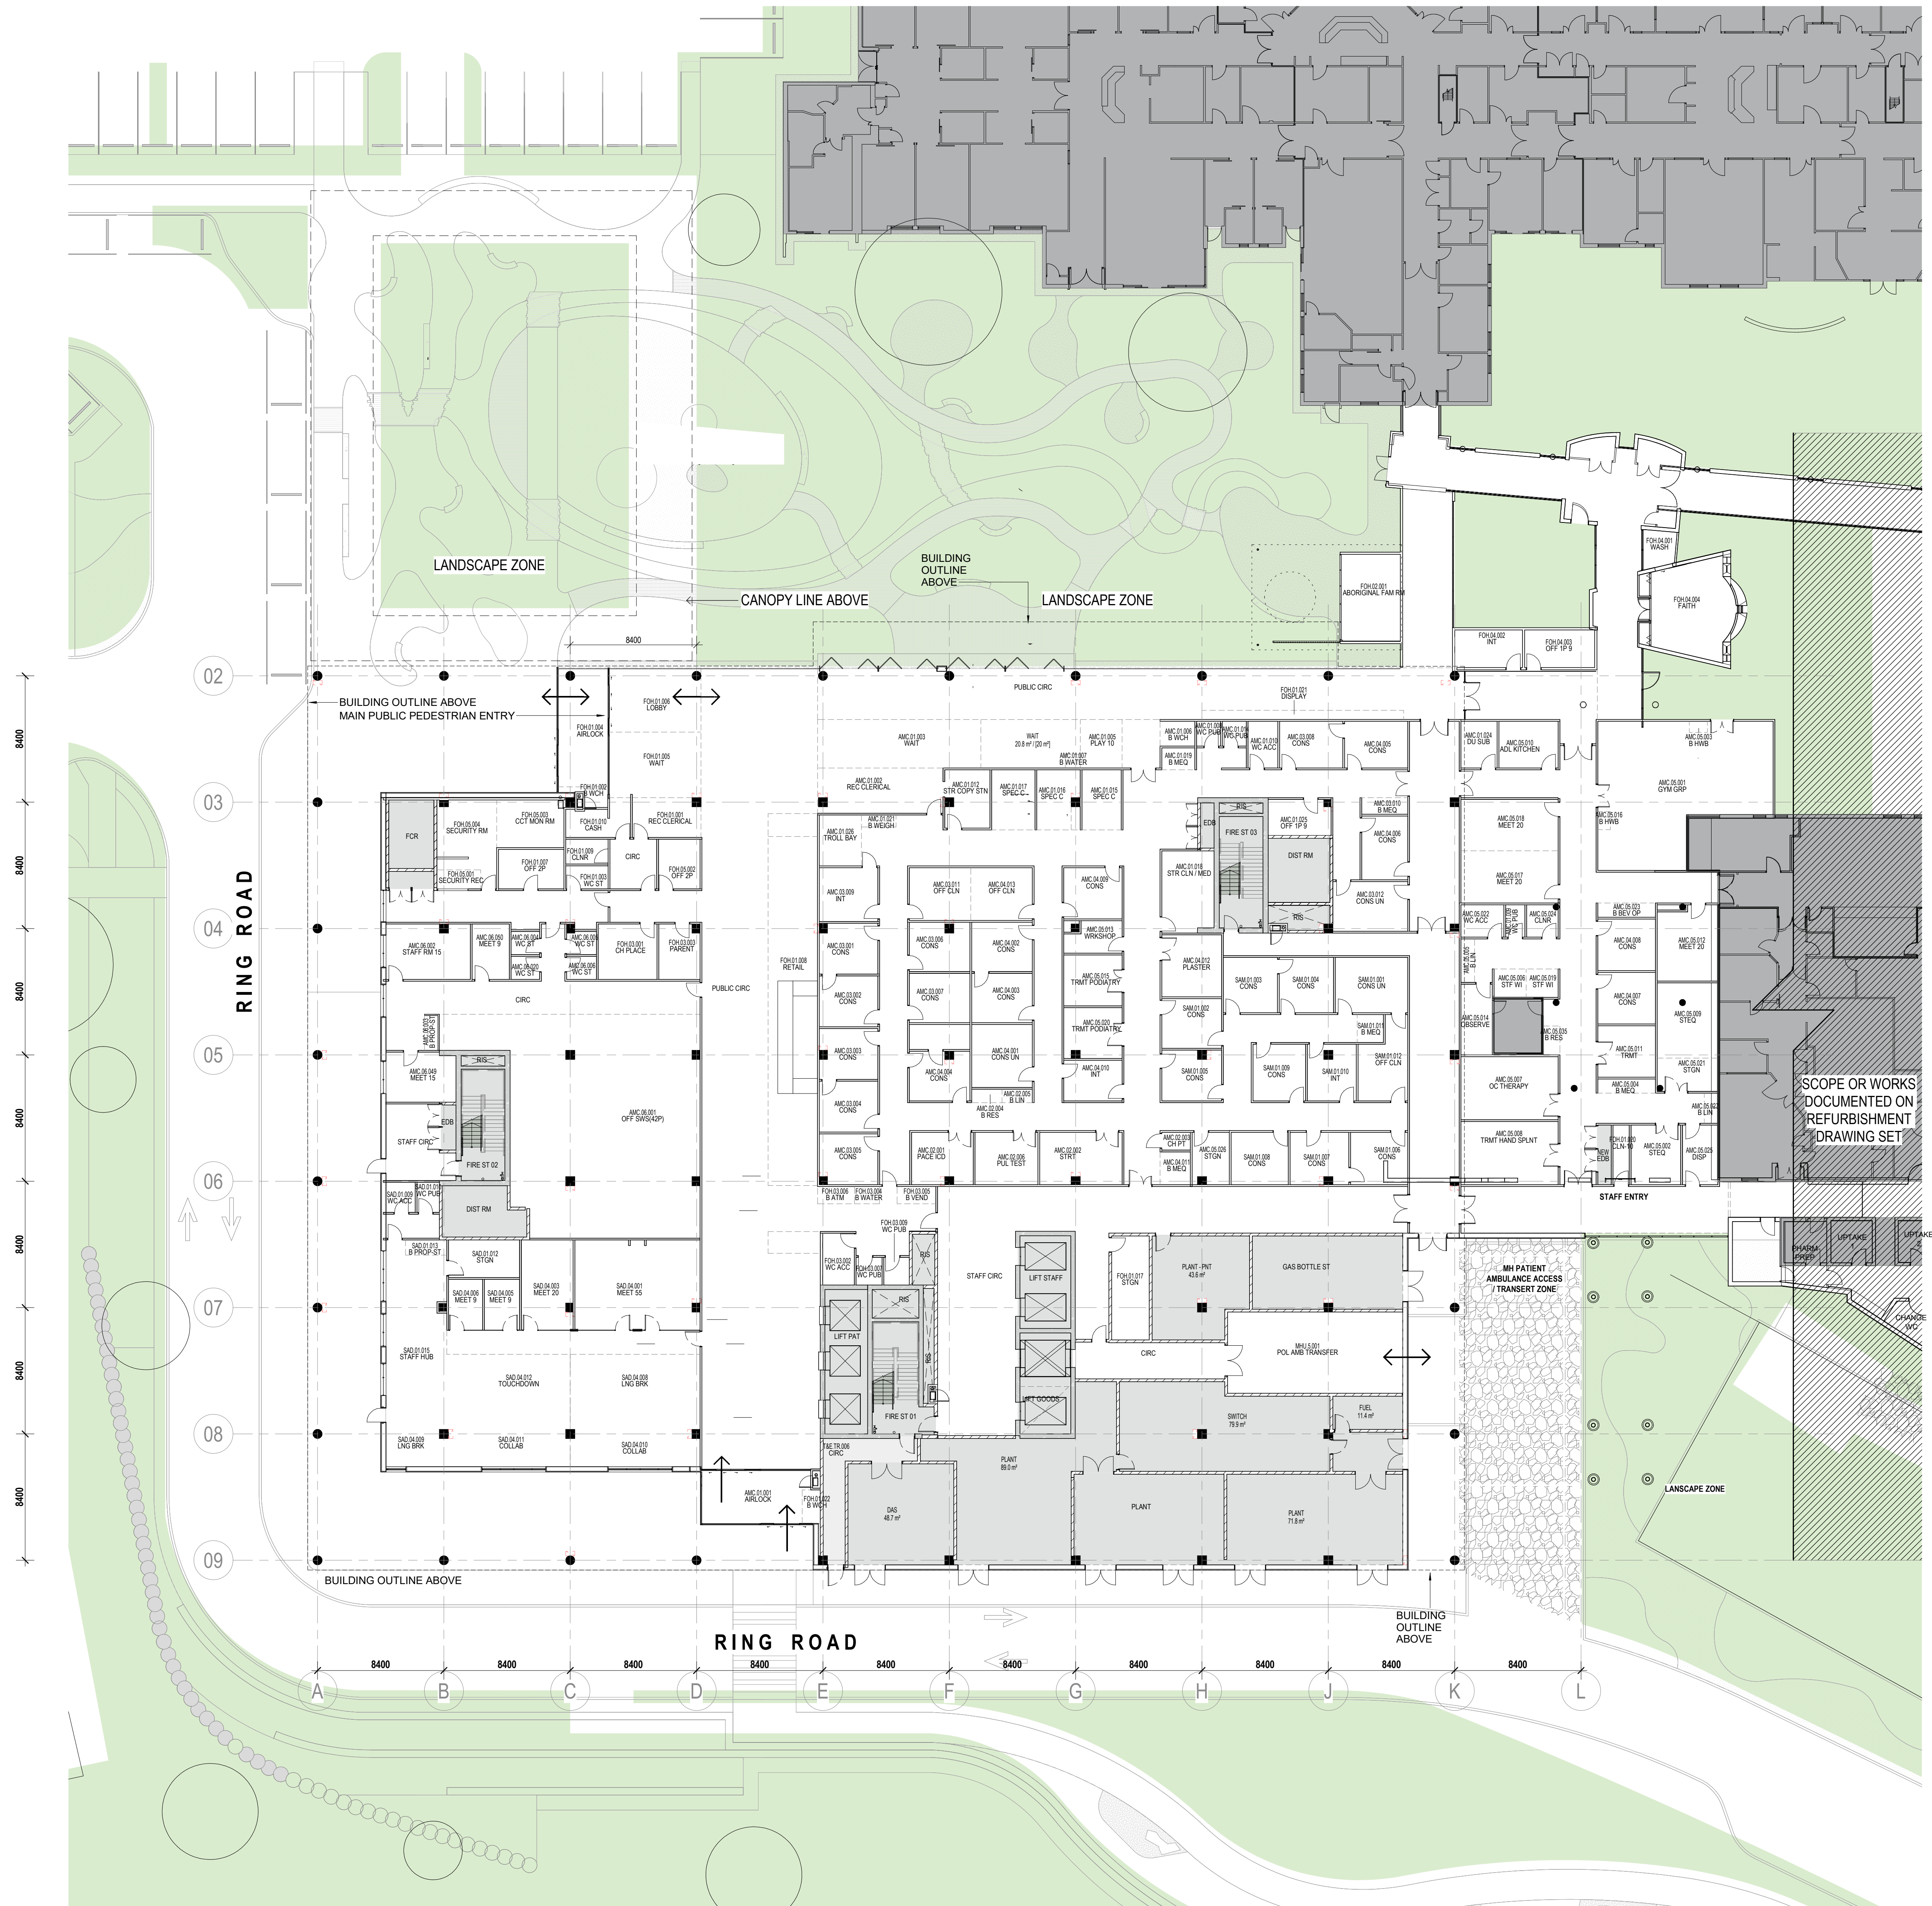

GA PLAN - L02

DEPARTMENT LEGEND:

CSB NEW BUILD

CORE, SERVICES & ENGINEERING

EXISTING BUILDING

ROOM TAG LEGEND:

MHU.3.017 -- ROOM NUMBER

ENS MH -- ROOM LABEL

5.4m (5m) -- P3 PROGRAMMED AREA IN M2

P3 DESIGN AREA IN M2

CONSULTANT

Hassell

Hassell LTD ABN 24 007 711 435
Level2, Pier 8/9, 23 Hickson Rd
Sydney NSW 2000 Australia
T +61 2 9101 2000
F +61 2 9101 2100
sydney@hassellstudio.com
Nominated Architects NSW
Tony Grant 5330
Gerrit Scott 6842
Ross de la Motte 7398

NOTES

1. Do not scale drawing. Written dimensions govern
 2. All dimensions are in millimeters unless noted otherwise
 3. All dimensions shall be verified on site before proceeding with the work. Hassell shall be notified in writing of any discrepancies.
 4. This drawing must be read in conjunction with all relevant contracts, specifications and drawings.
- This drawing is an uncontrolled copy. Unless noted otherwise
- © Copyright of this drawing is vested in Hassell Ltd.

REV DESCRIPTION

- | | |
|---|--------------------------|
| A | FOR INFORMATION - 50% CD |
| B | FOR INFORMATION - 75% CD |
| C | WIP CD |
| D | WIP CD |
| E | FOR INFORMATION |
| F | WIP - FOR INFORMATION |
| G | WIP - FOR INFORMATION |
| H | SCHEMATIC DESIGN |

DATE

- | |
|------------|
| 22/10/2023 |
| 21/11/2023 |
| 15/12/2023 |
| 23/02/2024 |
| 09/04/2024 |
| 23/07/2024 |
| 12/08/2024 |
| 19/12/2024 |

CLIENT

Health Infrastructure NSW

PROJECT

Albury Wodonga Regional Hospital
Project - CSB
201 Borella Road, East Albury

STATUS

SCHEMATIC DESIGN

DRAWING TITLE

GA FLOOR PLAN - LEVEL 2 - ENTRY

REVIEWED

RP

APPROVED

CL

DRAWING NO.
AWH-HSL-AR-MW-CSB-
03-DWG-02001

SCALE @ A0

As indicated

PROJECT NO.

016713

REV NO.

H